


## **Localizacion en el Municipio de Sosua**



Localizacion en la Republica Dominicana



# Localización en el Caribe

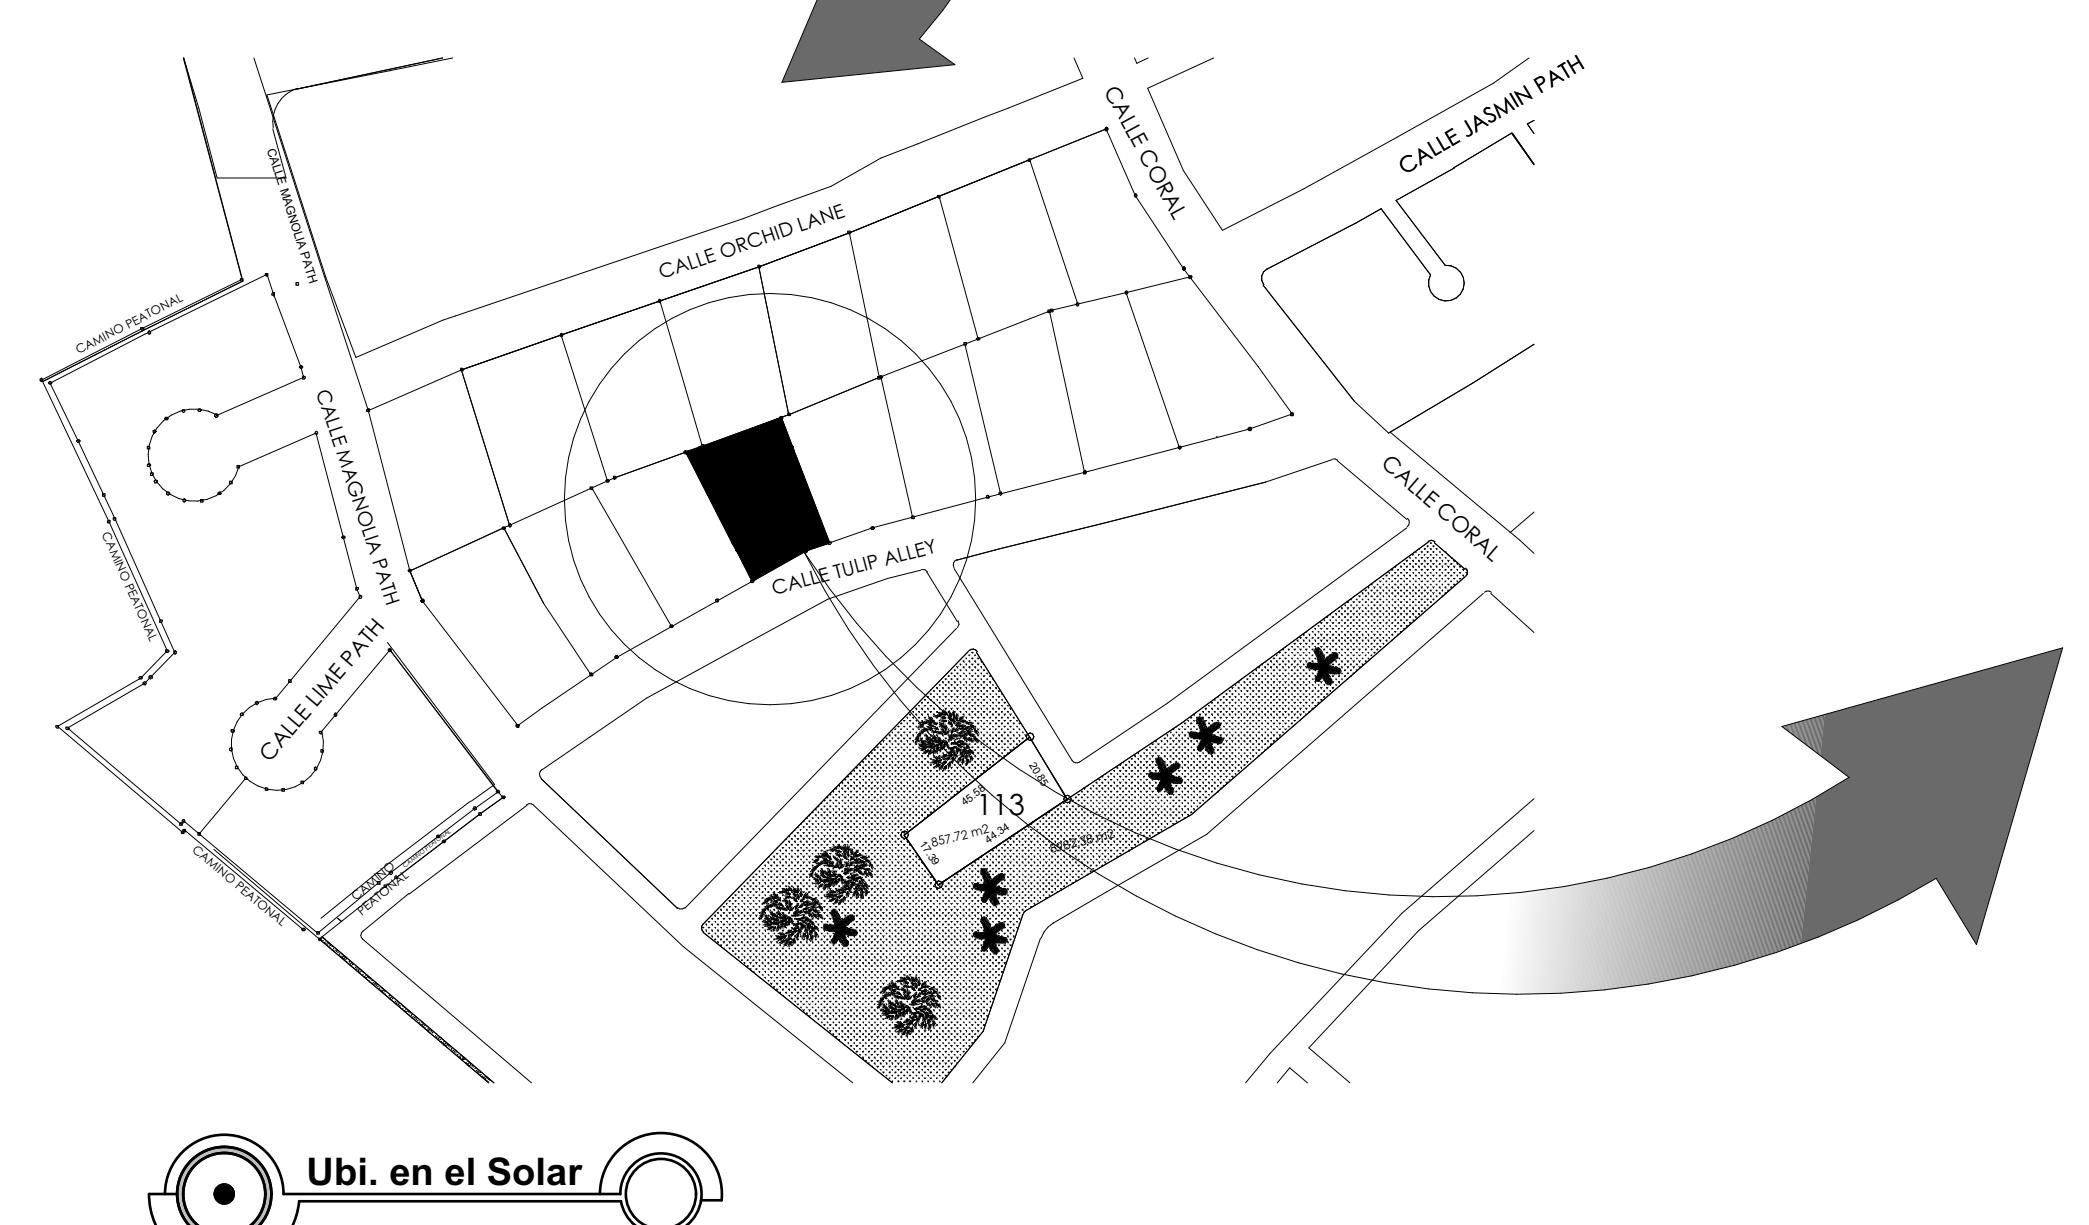

INDIC

ARQUITECTONICO

- ## ARQUITECTONICO

## **ESTRUCTURA**

- 06/11 Plano Estruc. de Cimientos + Detalles.  
07/11 Plano Estruc. de techo + Detalles.**



## ELECTRICAS

- ## **08/11 Plano Inst. Elect. Tomacorrientes + Detalles**

## **09/11 Plano Inst. Elect. Luminarias + Detalles.**

## SANITARIAS

- 10/11 Plano Inst. Agua Potable.  
11/11 Plano Inst. Sanitaria + Detalle R.A.F.A.**

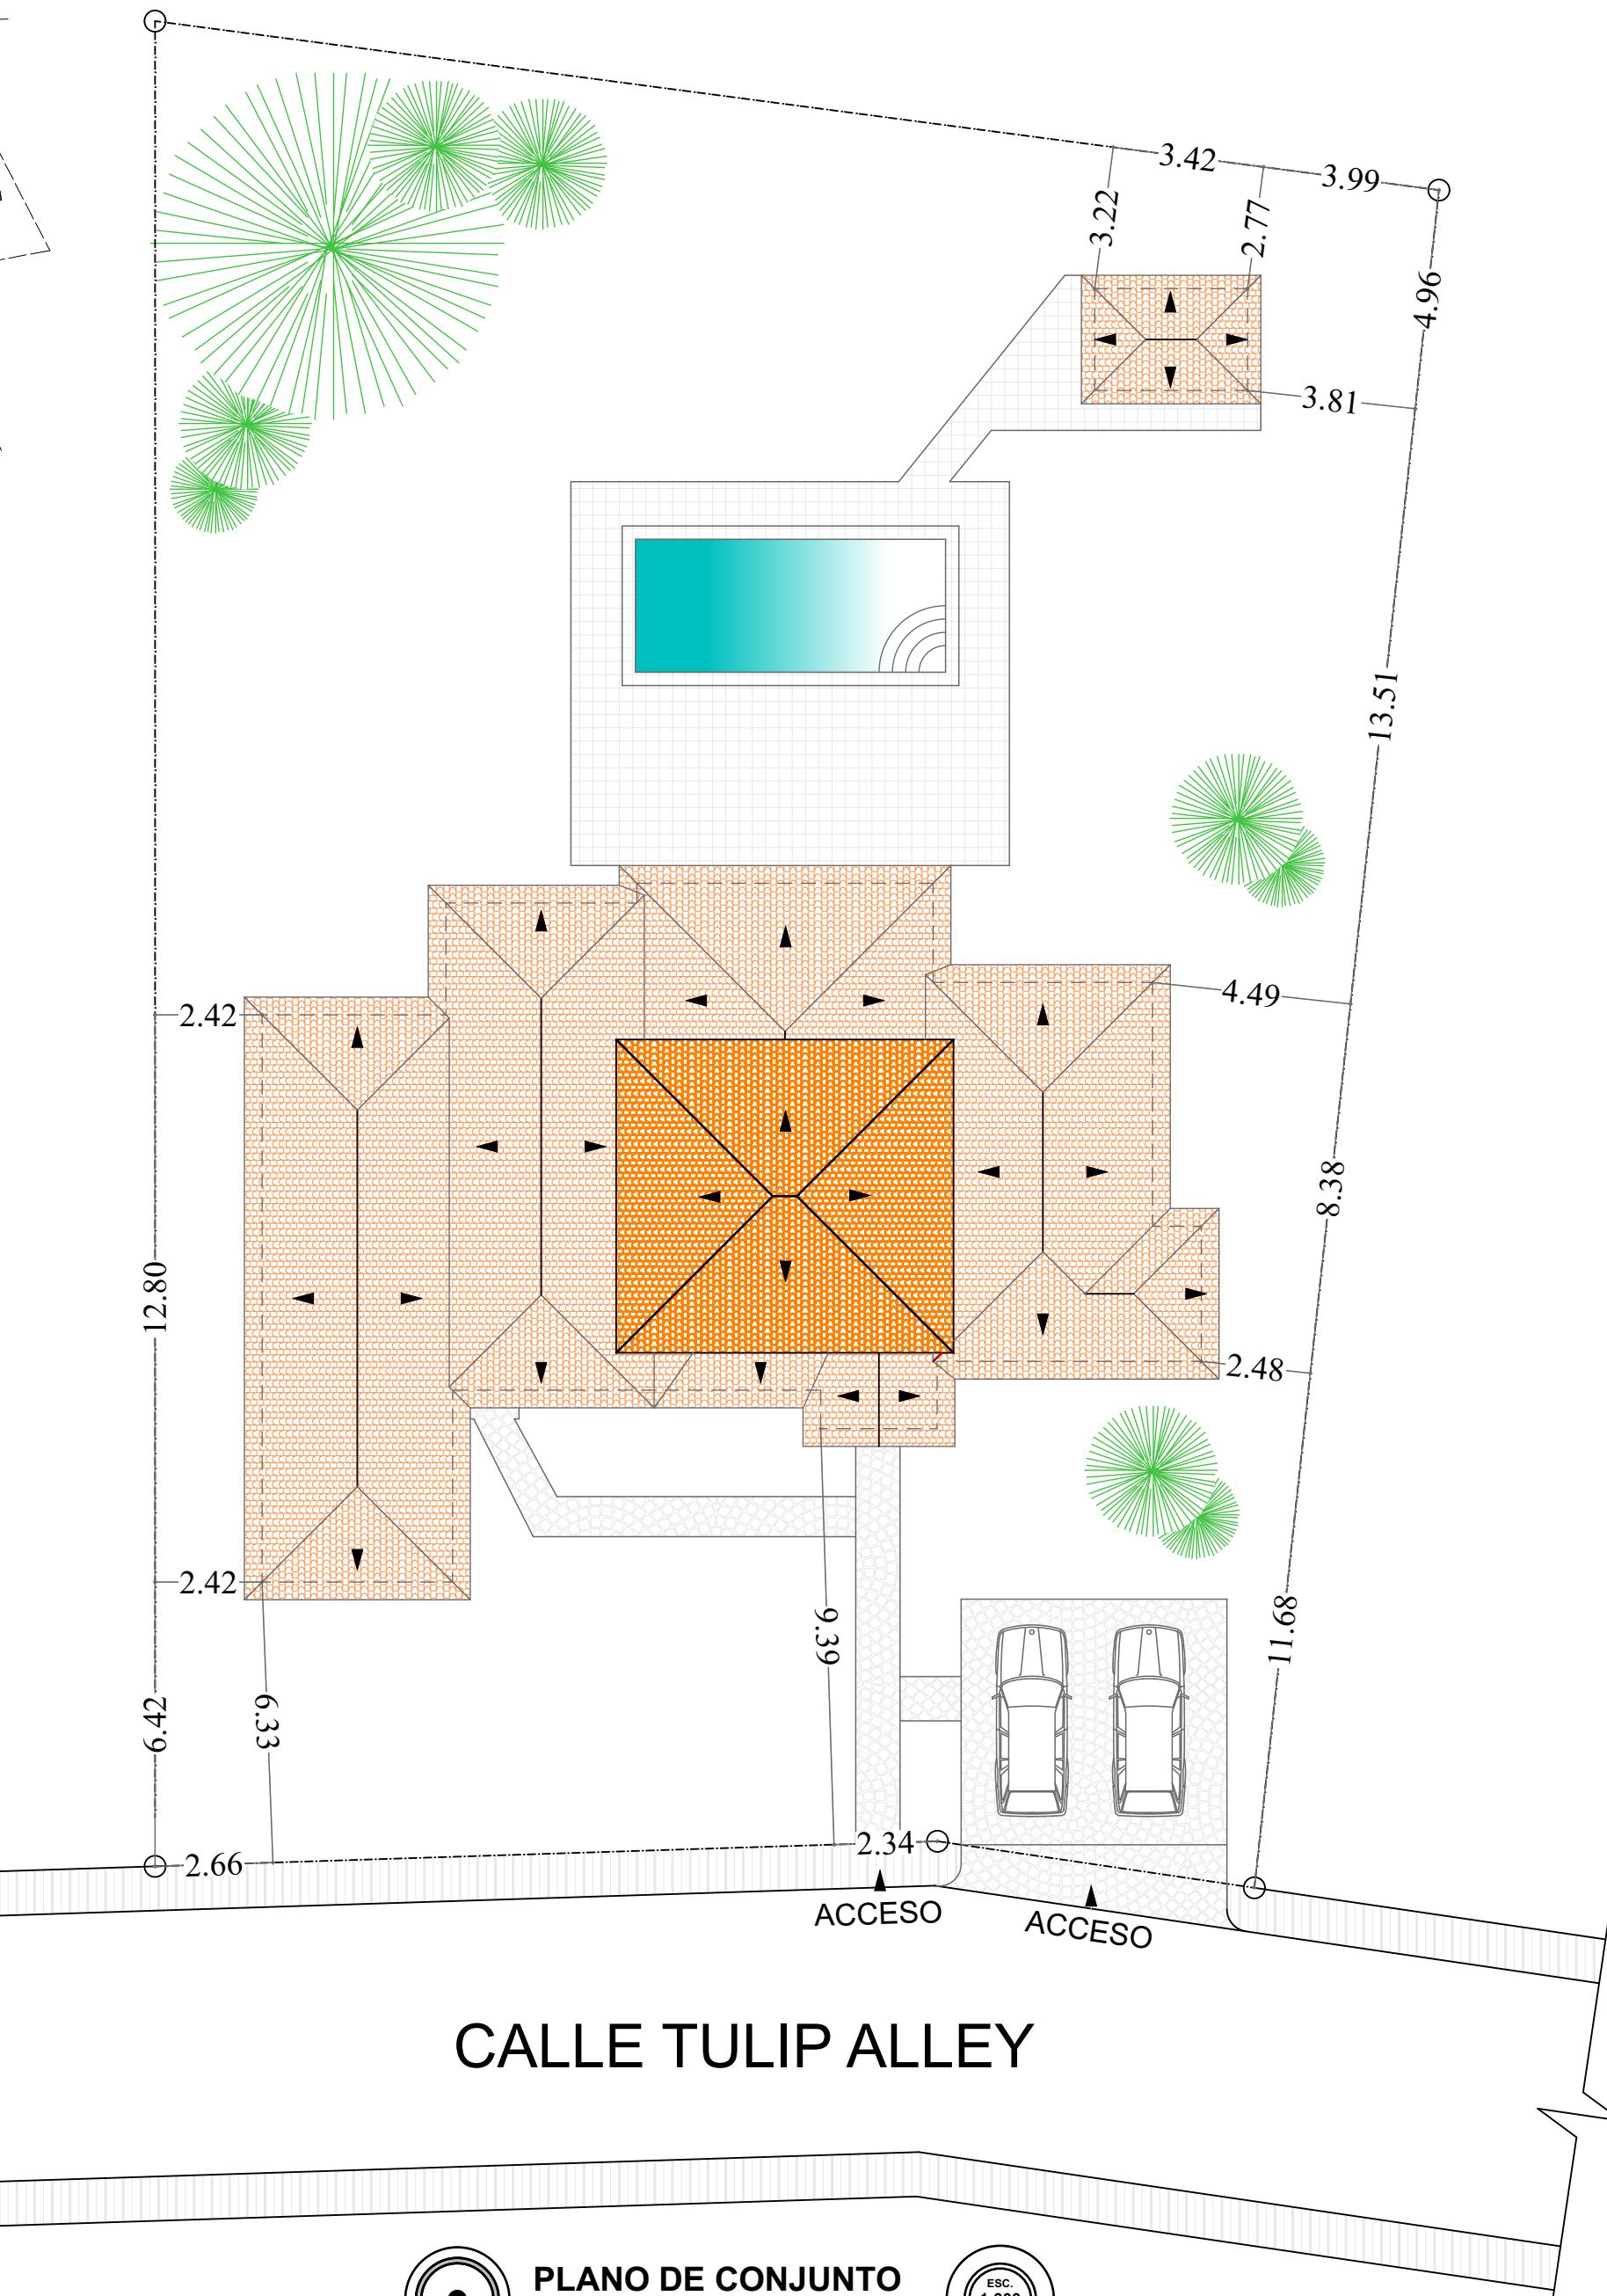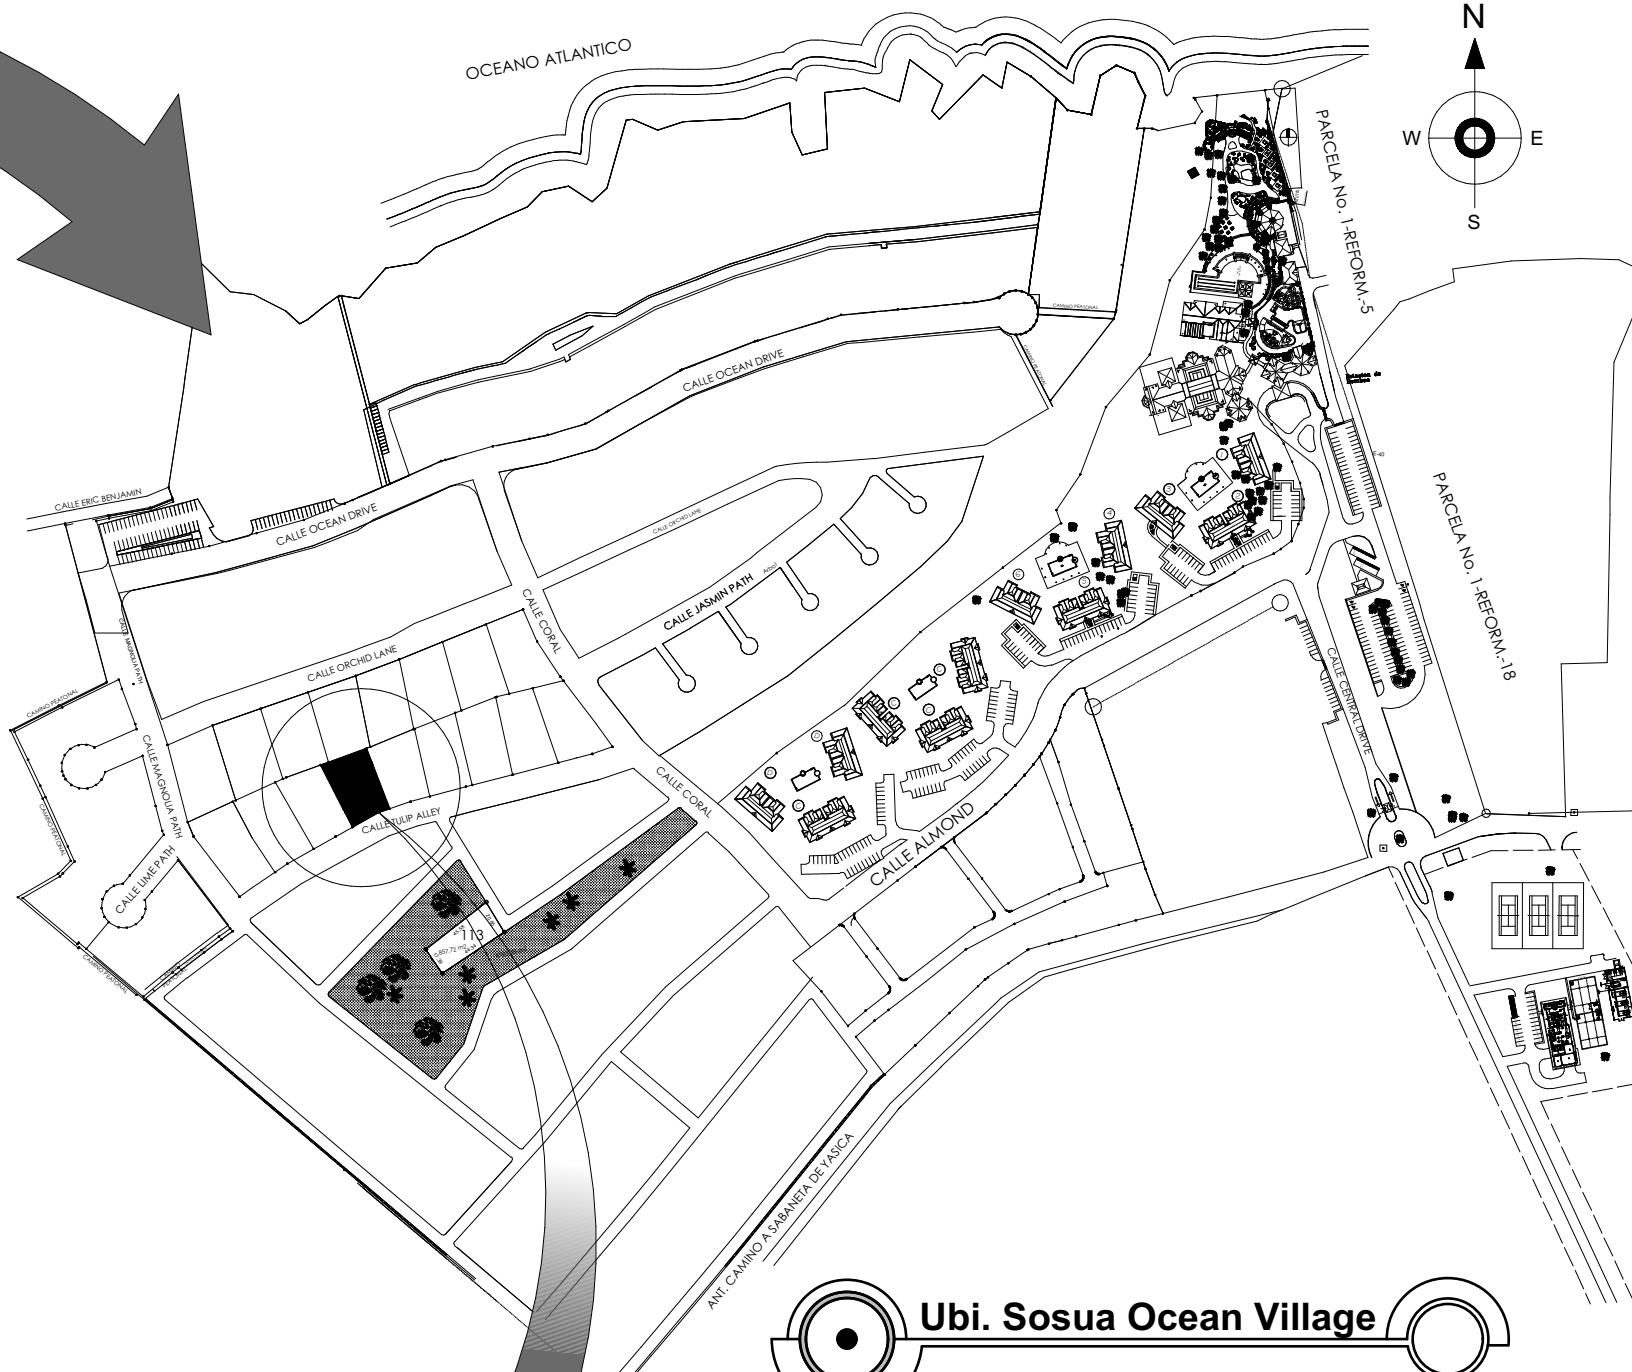

CALLE TULIP ALLEY

PLANO DE CONJUNTO

# **Ficha Técnica**

DIS. ARQUITECTONICO	CODIA
ARQ. ERISS ESPINAL	19346
DIS. ESTRUCTURAL	CODIA
ING. JOAQUIN BOLIVAR ALMANZAR	8608
DIS. ELECTRICO	CODIA
ING. HECTOR HERNANDEZ	18559
DIS. SANITARIO	CODIA
ARQ. ERISS ESPINAL	19346
DIGITACION	CODIA
ARQ. ESTEBAN DEOGRACIA	37644
COORDINACION Y REVISION	CODIA
ARQ. ESTEBAN DEOGRACIA	37644
RESPONSABLE DEL PROYECTO	CODIA

## PROYECTO **Casa Yuri y Marina**

## **UBICADO EN: Sosua- Cabarete Sosua Ocean Village**

## **CONTENIDO :**

### **Localizacion y Ubicacion + Plano de Conjunto + Desague de Techos**



## **REFERENCIA DE PLANOS :**

### **Plano Terminado**

**FECHA :**  
**Marzo/2020**

## **ESCALA: Indicada**



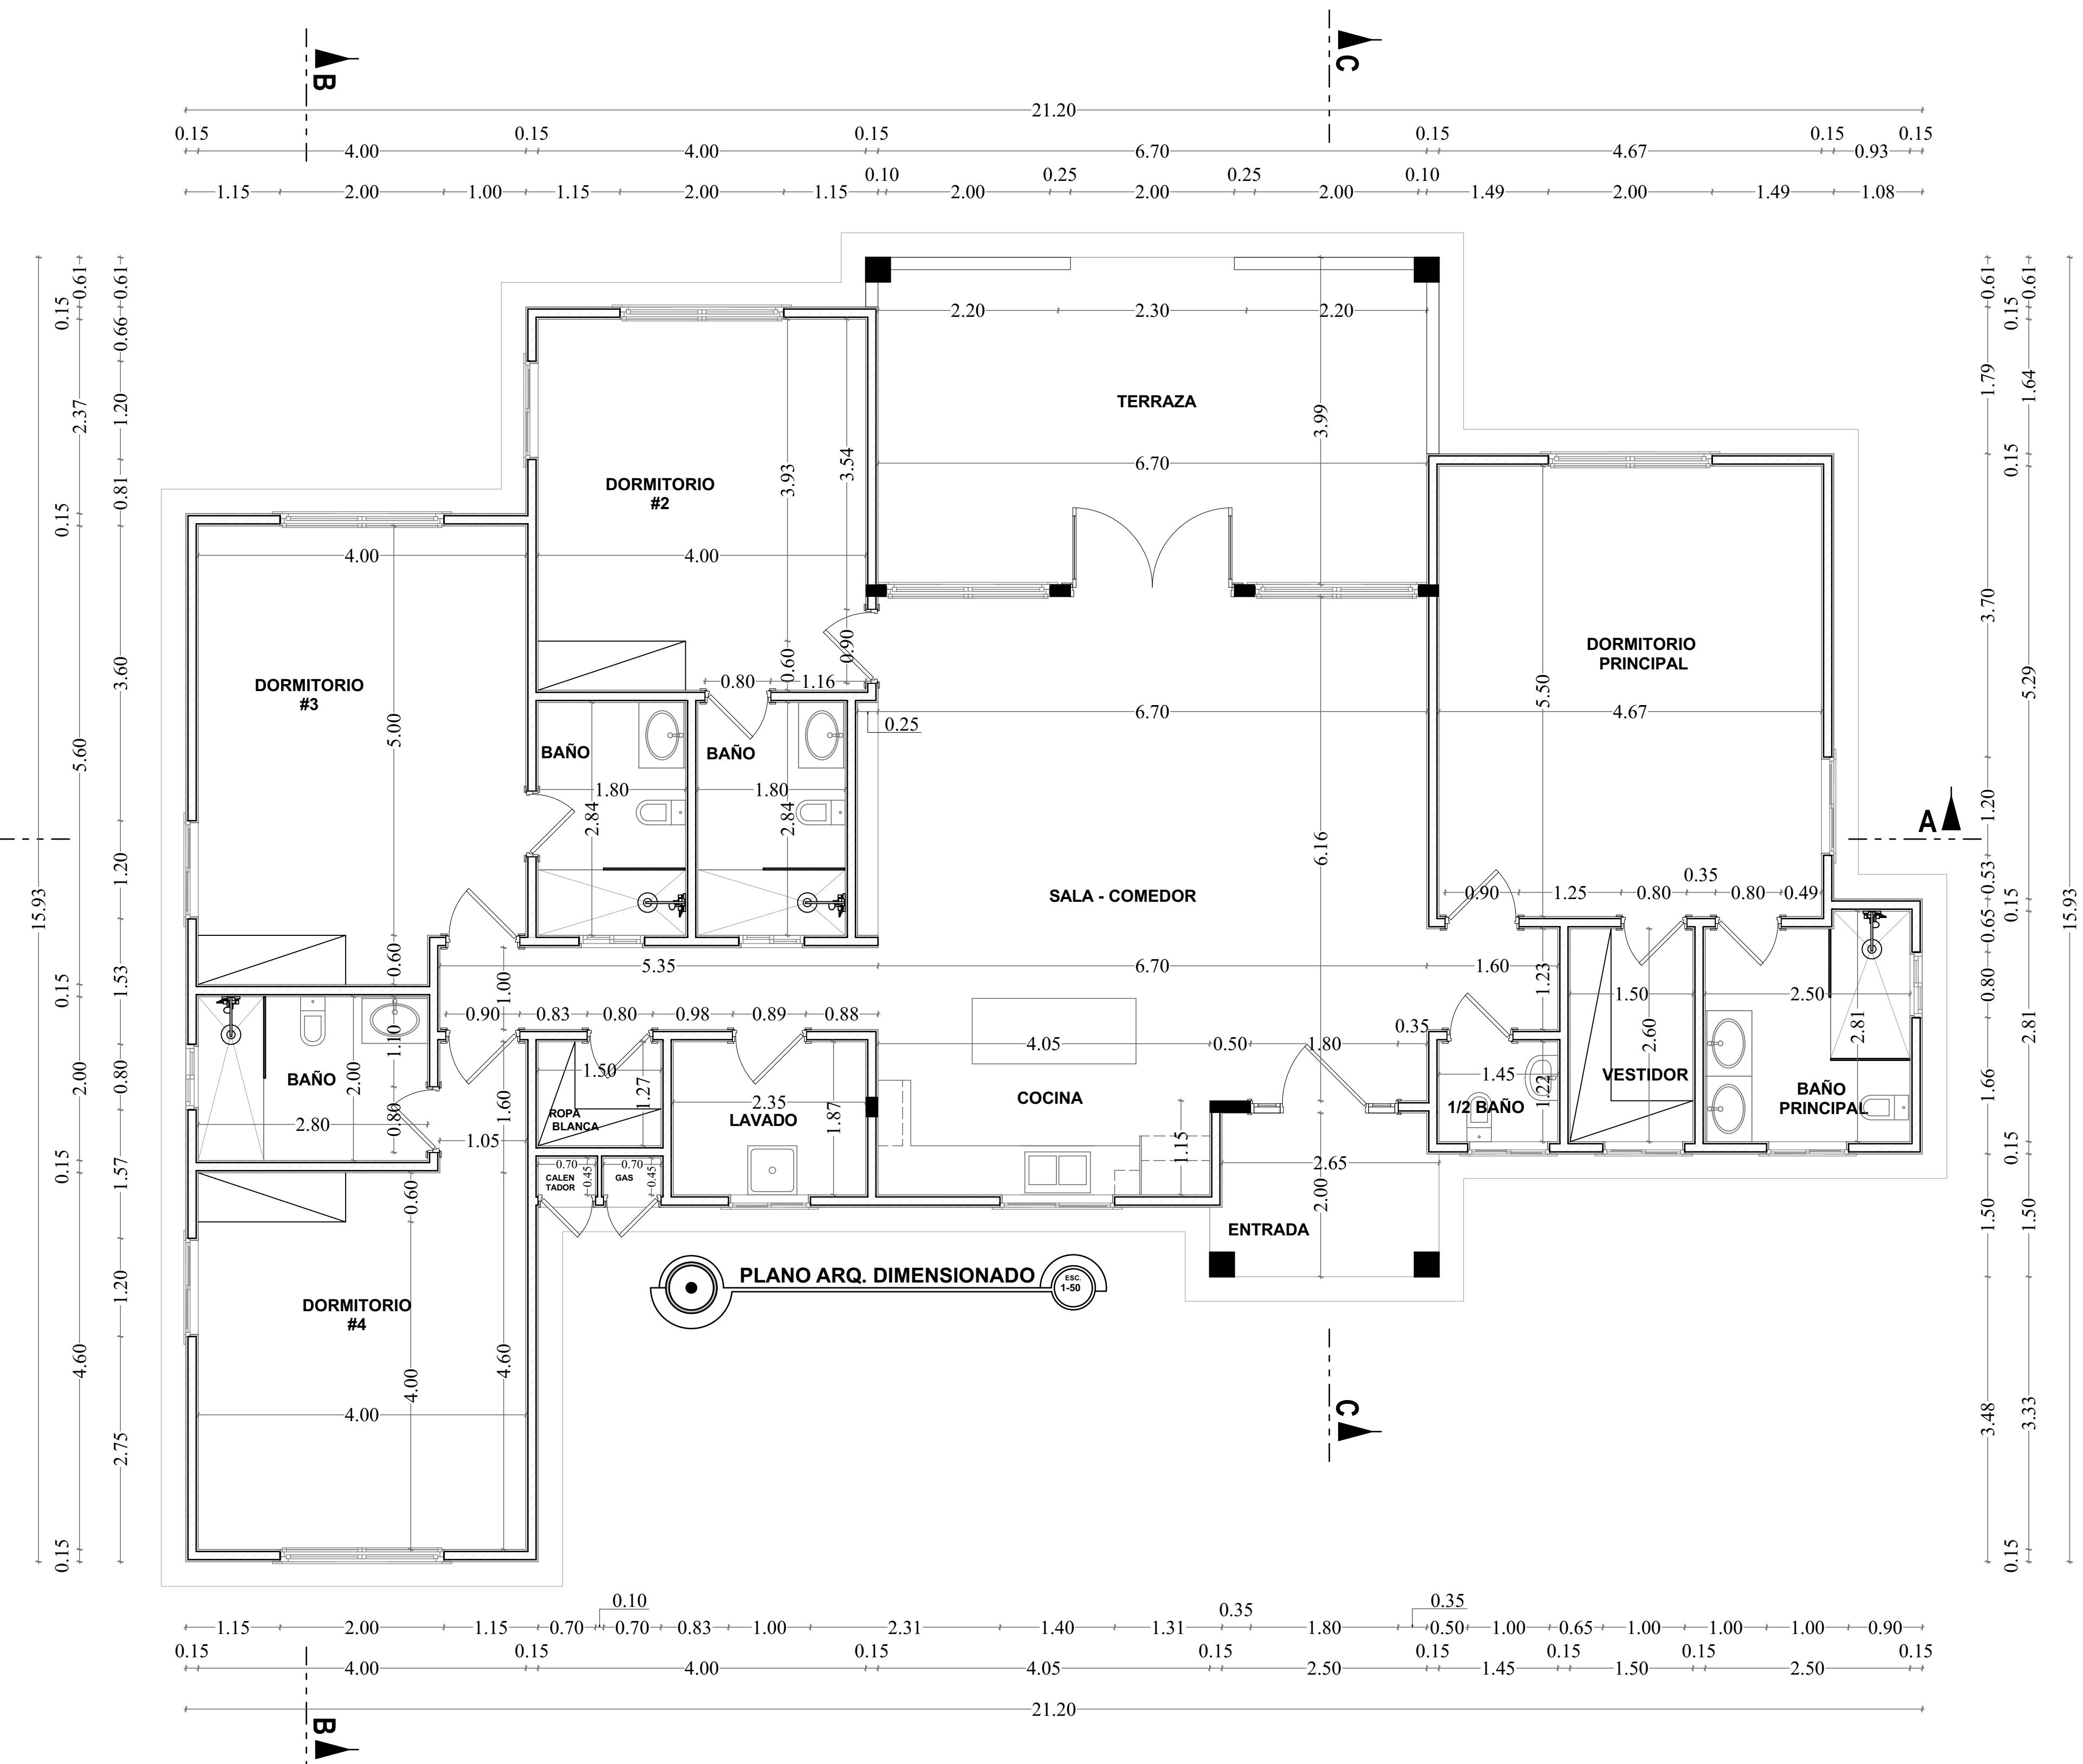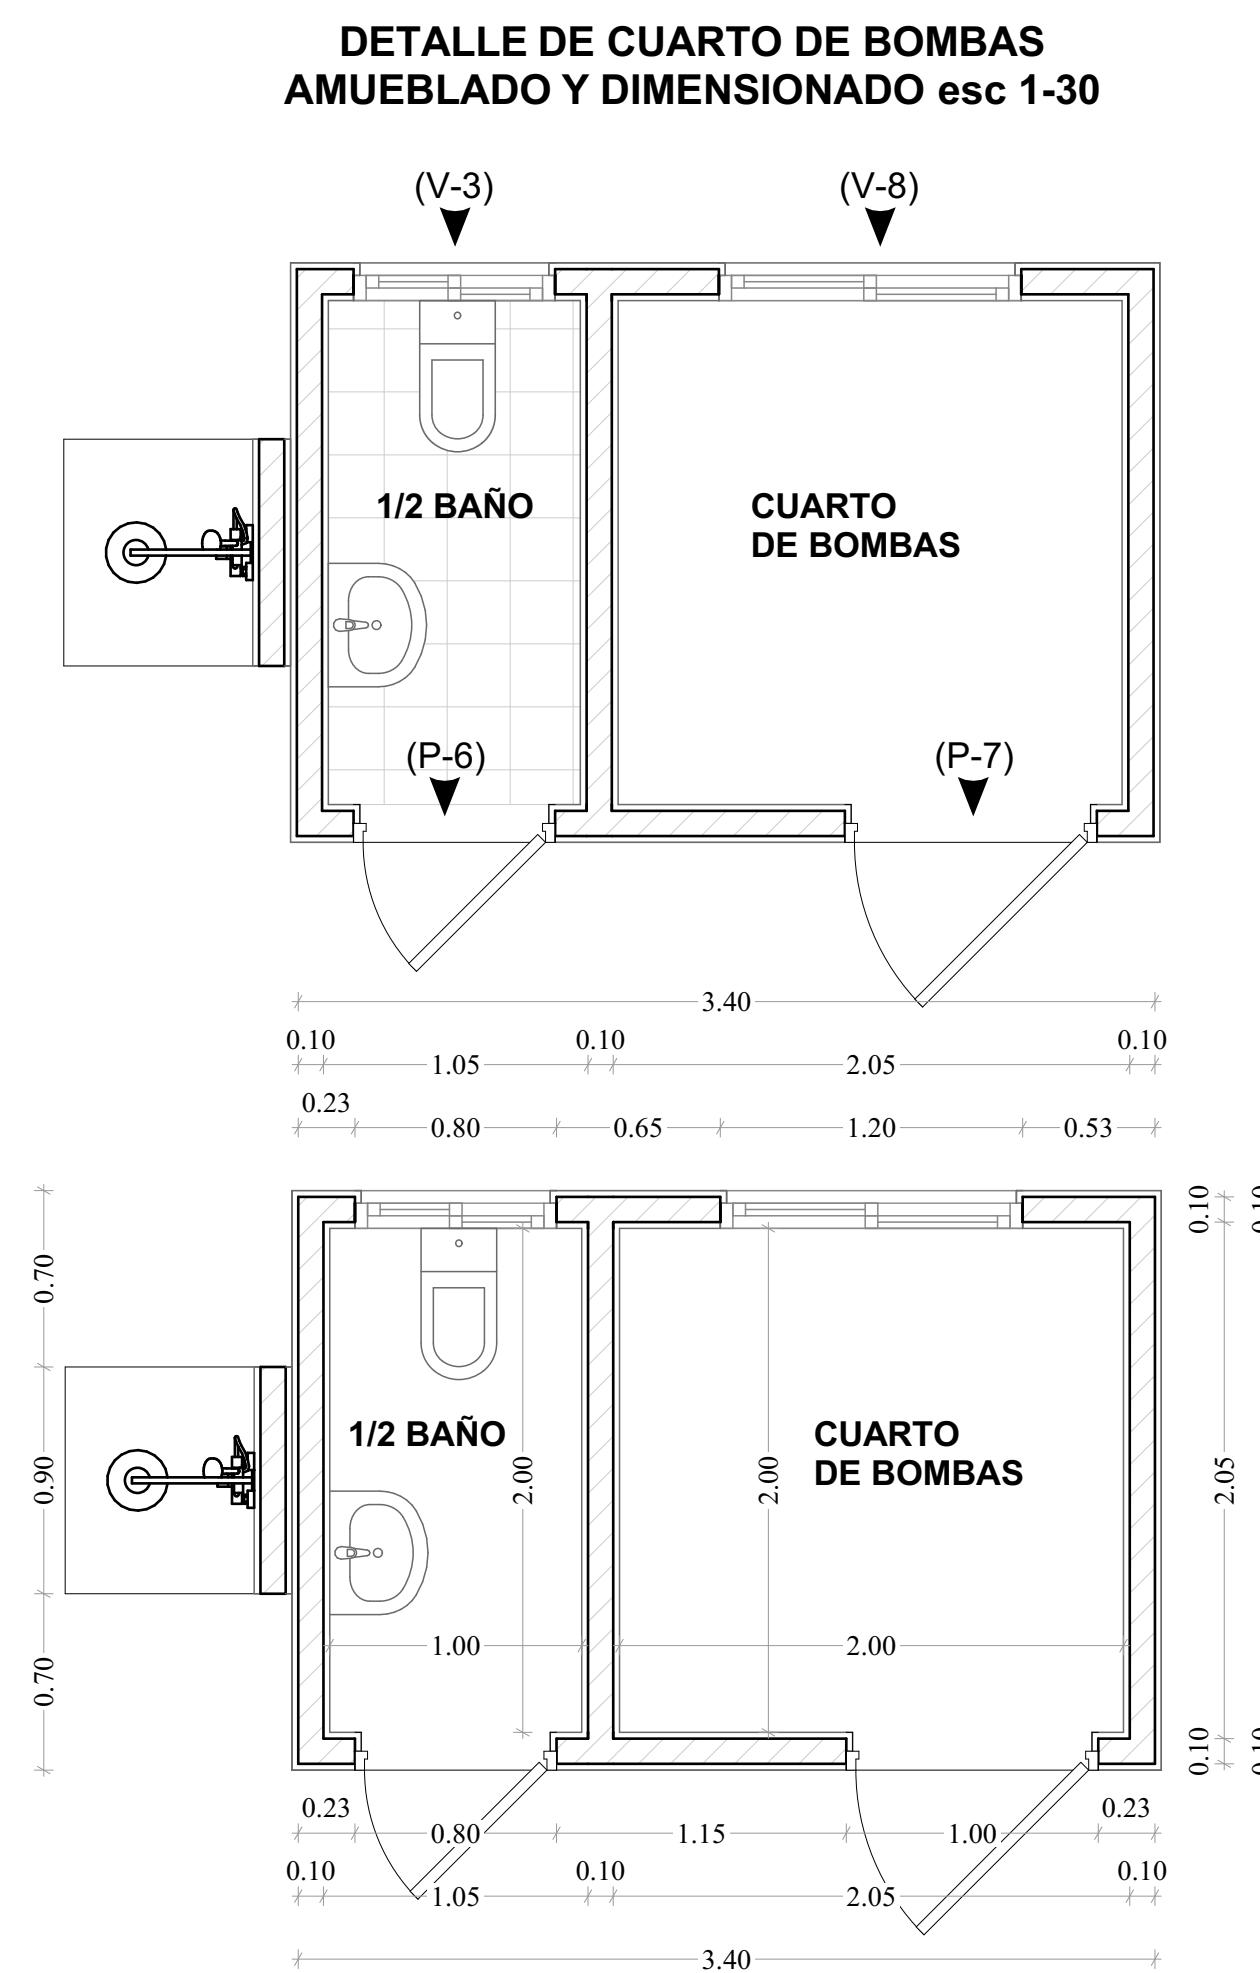

# **Ficha Técnica**

DIS. ARQUITECTONICO	CODIA
ARQ. ERIS ESPINAL	19346
DIS. ESTRUCTURAL	CODIA
ING. JOAQUIN BOLIVAR ALMANZAR	8608
DIS. ELECTRICO	CODIA
ING. HECTOR HERNANDEZ	18559
DIS. SANITARIO	CODIA
ARQ. ERIS ESPINAL	19346
DIGITACION	CODIA
ARQ. ESTEBAN DEOGRACIA	37644
COORDINACION Y REVISION	CODIA
ARQ. ESTEBAN DEOGRACIA	37644
RESPONSABLE DEL PROYECTO	CODIA

# PROYECTO **Casa Yuri y Marina**

**UBICADO EN: Sosua- Cabarete**

## **INTENIDO :**


## **REFERENCIA DE PLANOS :**

### **Plano Terminado**

HA :  
zo/2020


**KALA: Indicada**



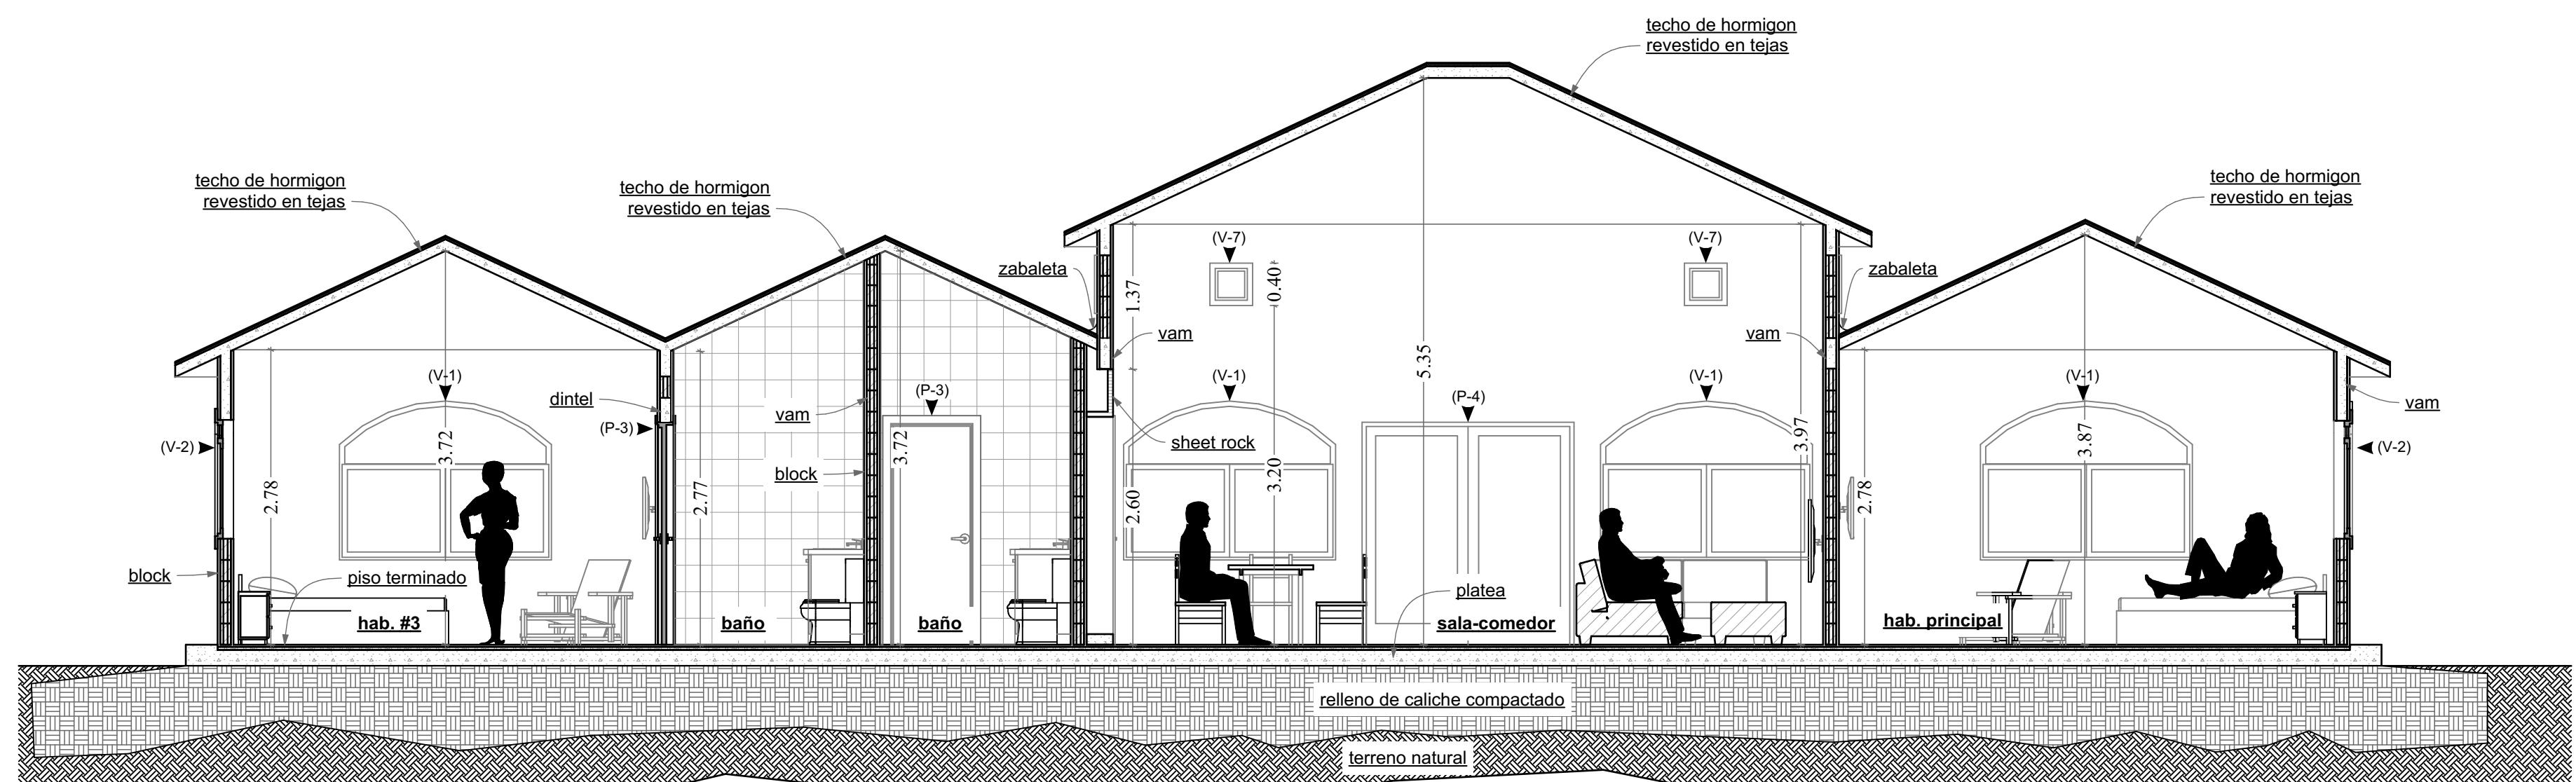


**SECCION A-A'**

ESC.  
1-50

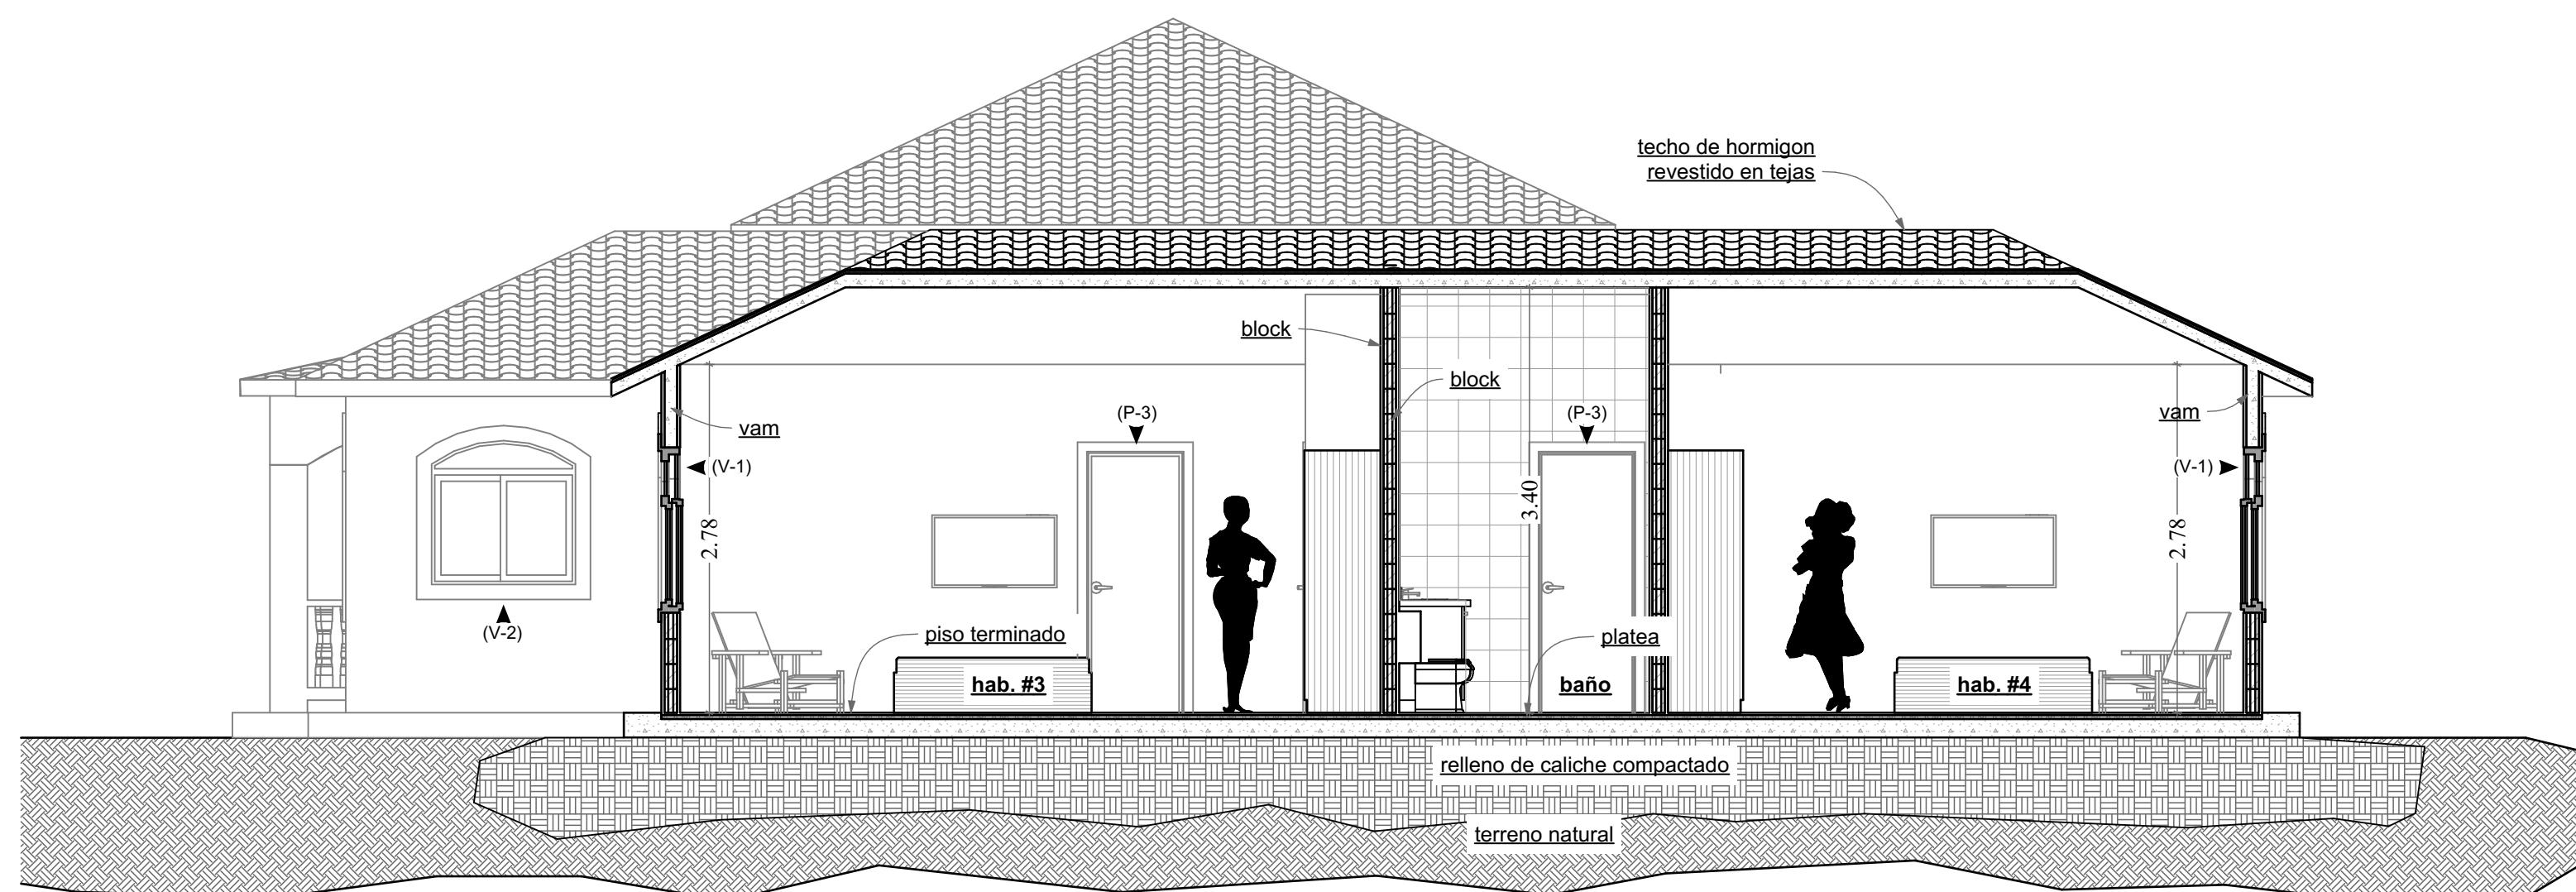



## SECCION B-B'

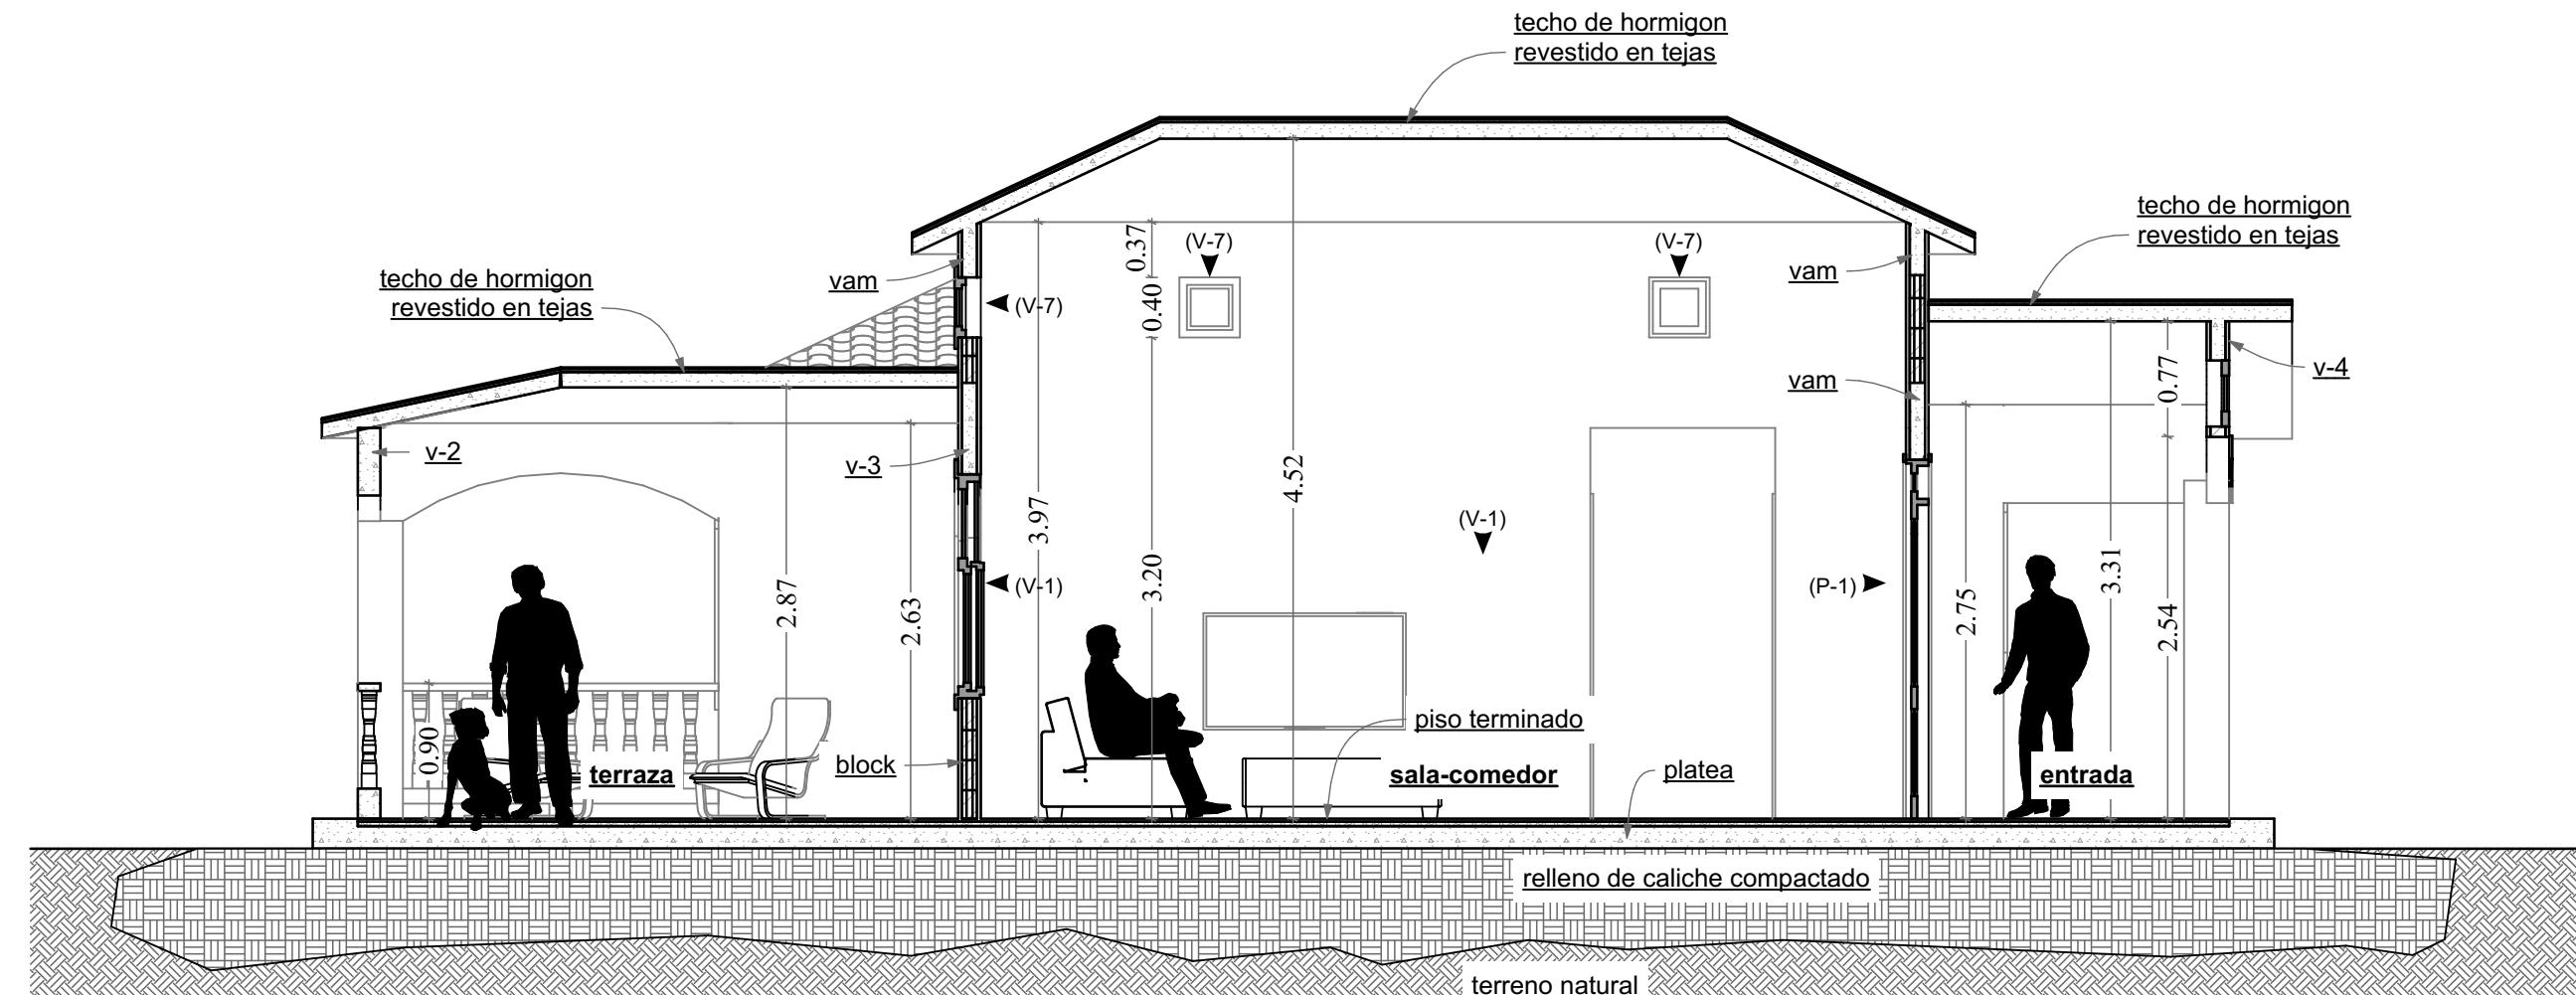

# **Ficha Técnica**

DIS. ARQUITECTONICO	CODIA
ARQ. ERISSPINAL	19346
DIS. ESTRUCTURAL	CODIA
ING. JOAQUIN BOLIVAR ALMANZAR	8608
DIS. ELECTRICO	CODIA
ING. HECTOR HERNANDEZ	18559
DIS. SANITARIO	CODIA
ARQ. ERISSPINAL	19346
DIGITACION	CODIA
ARQ. ESTEBAN DEOGREGACIA	37644
COORDINACION Y REVISION	CODIA
ARQ. ESTEBAN DEOGREGACIA	37644
RESPONSABLE DEL PROYECTO	CODIA

## PROYECTO **Casa Yuri y Marina**

**UBICADO EN: Sosua- Cabarete  
Sosua Ocean Village**

## **CONTENIDO :**


### **secciones**

## **PROPIETARIO :**

## **FERENCIA DE PLANOS : ano Terminado**

ECHA :  
marzo/2020

### **SCALA: Indicada**

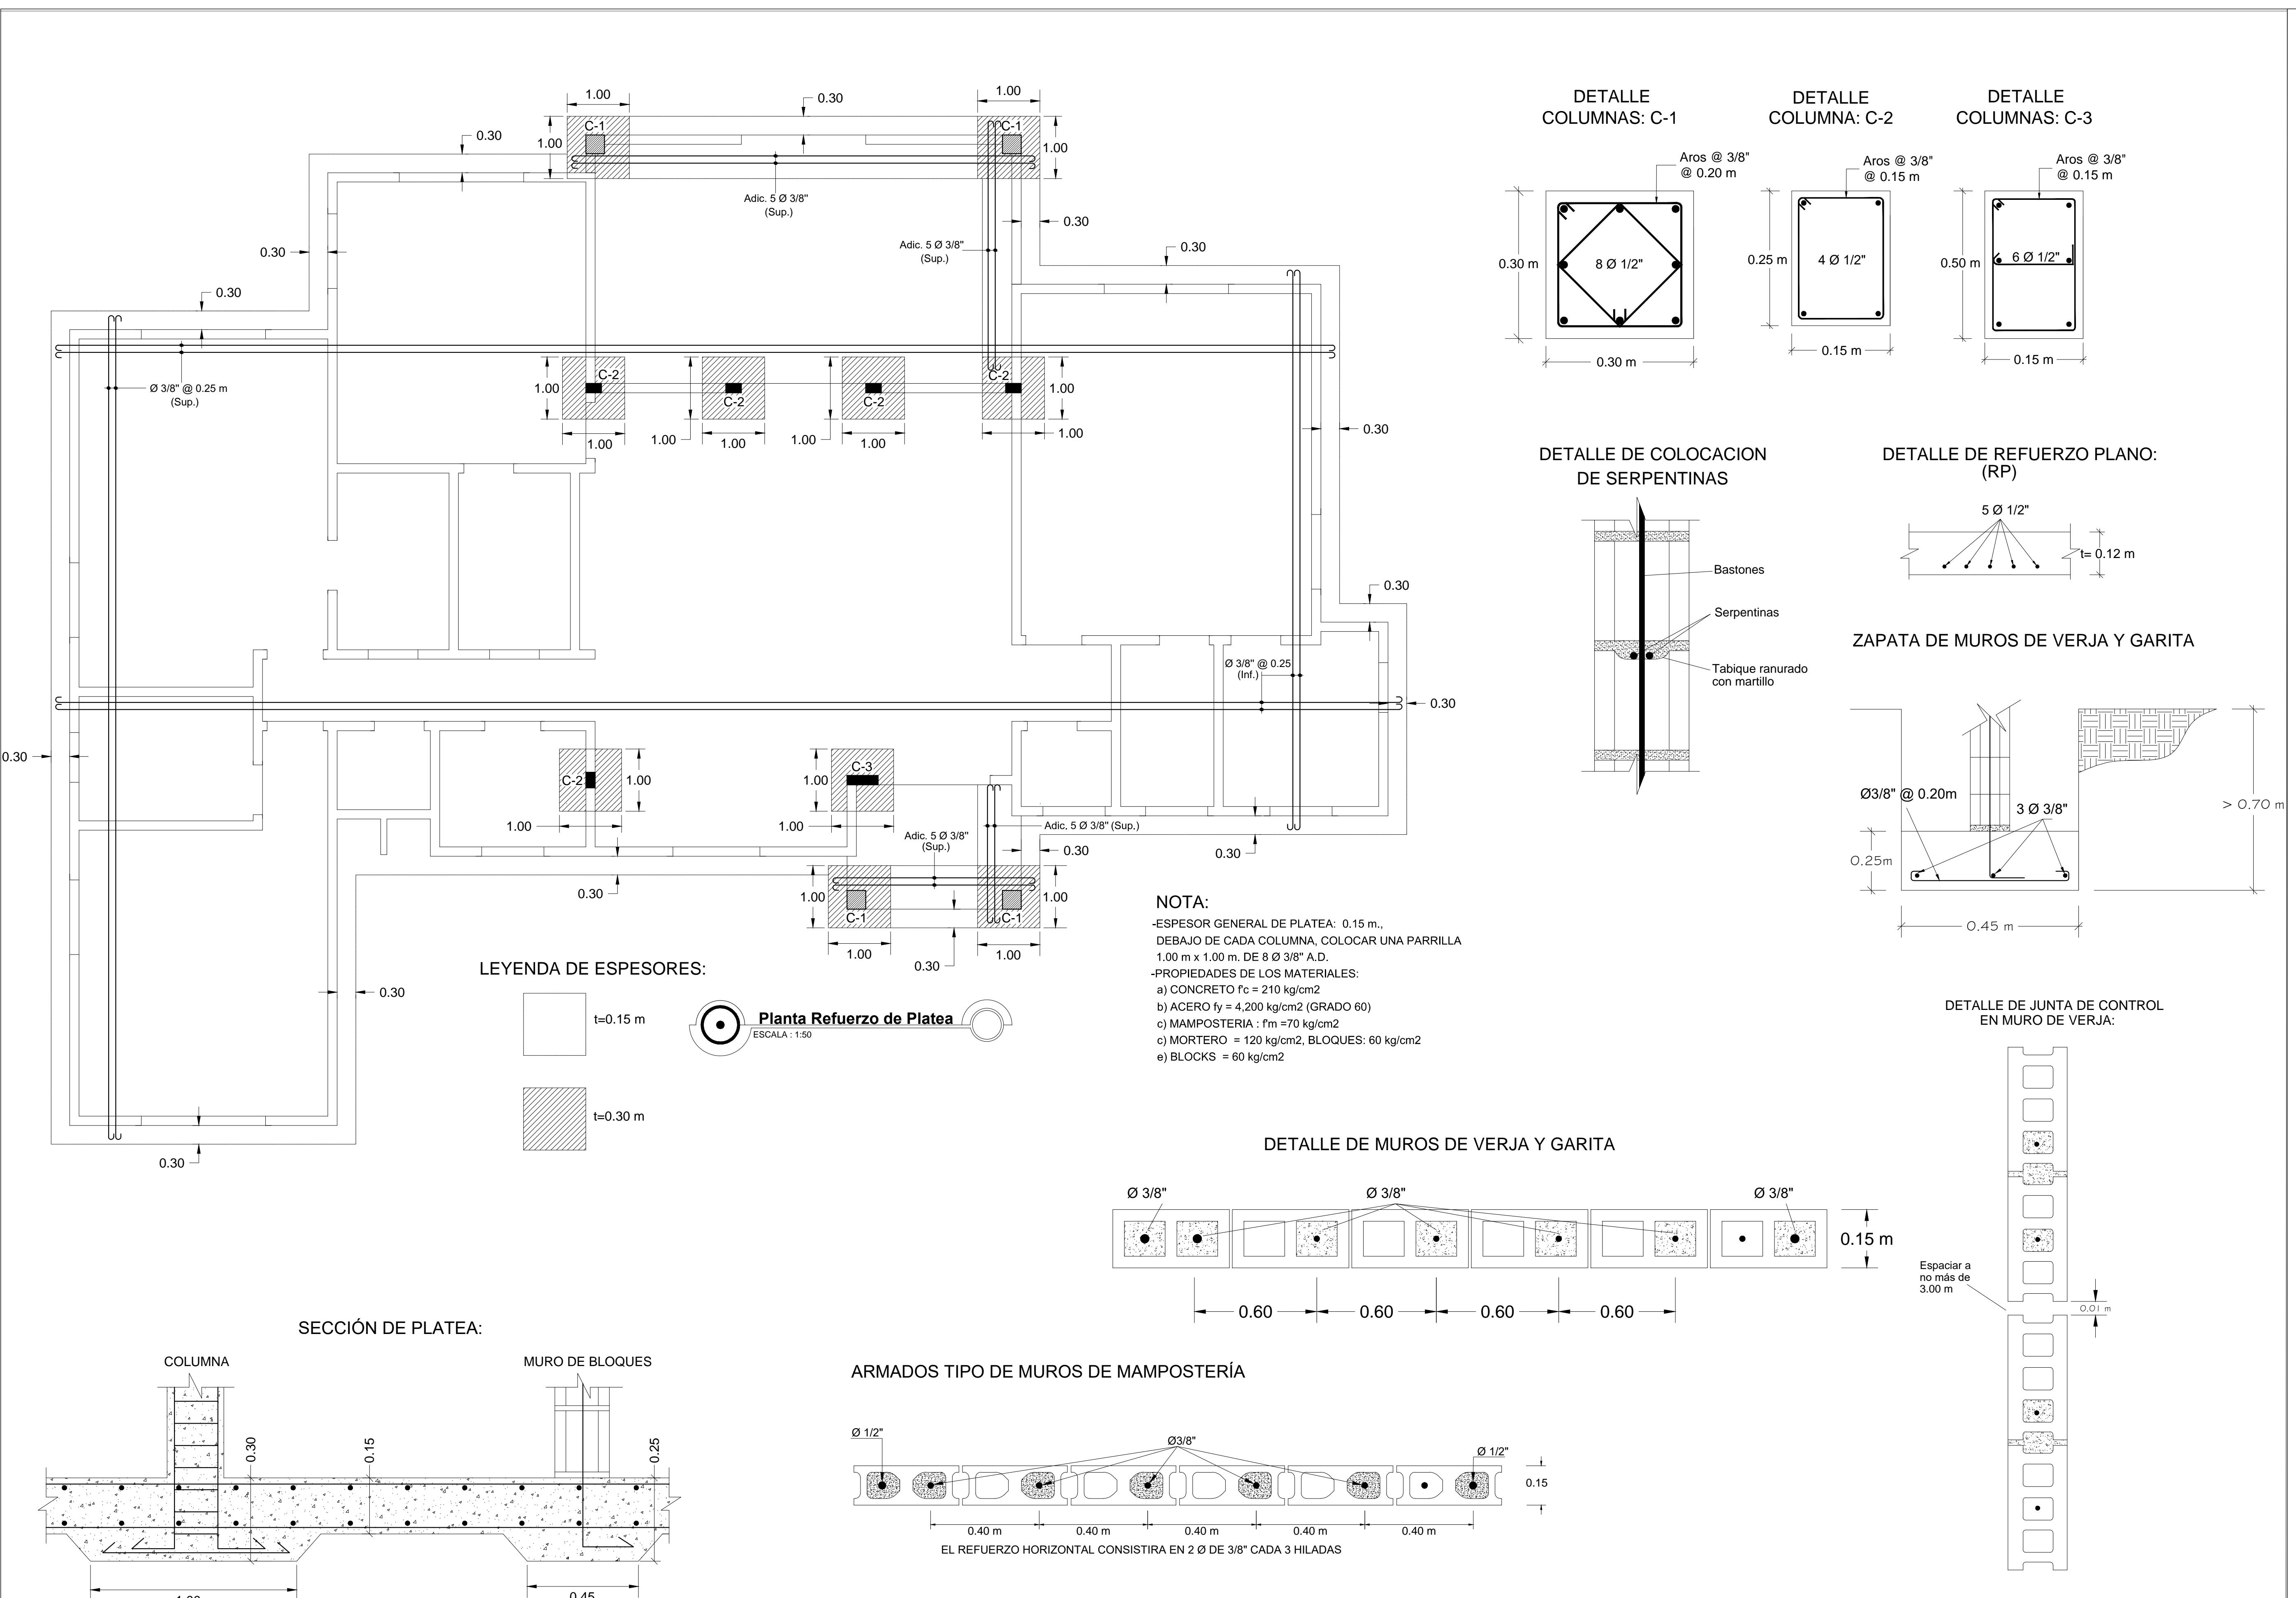

# **Ficha Técnica**

ECTONICO	CODIA
ESPINAL	19346
CTURAL	CODIA
JIN BOLIVAR ALMANZAR	8608
RICO	CODIA
OR HERNANDEZ	18559
RIO	CODIA
ESPINAL	19346
BAN DEOGRAZIA	CODIA
ON Y REVISION	CODIA
EPLAN DEOGRAZIA	37644
LE DEL PROYECTO	CODIA

PROYECTO  
soc. Yuri u. Marina

**DO EN: Sosua- Cabarete**  
**Sosua Ocean Village**

#### **de Cimentación + Detalles**


10. The following table summarizes the results of the study.

100%  


## DE PLANOS :

### ado

6

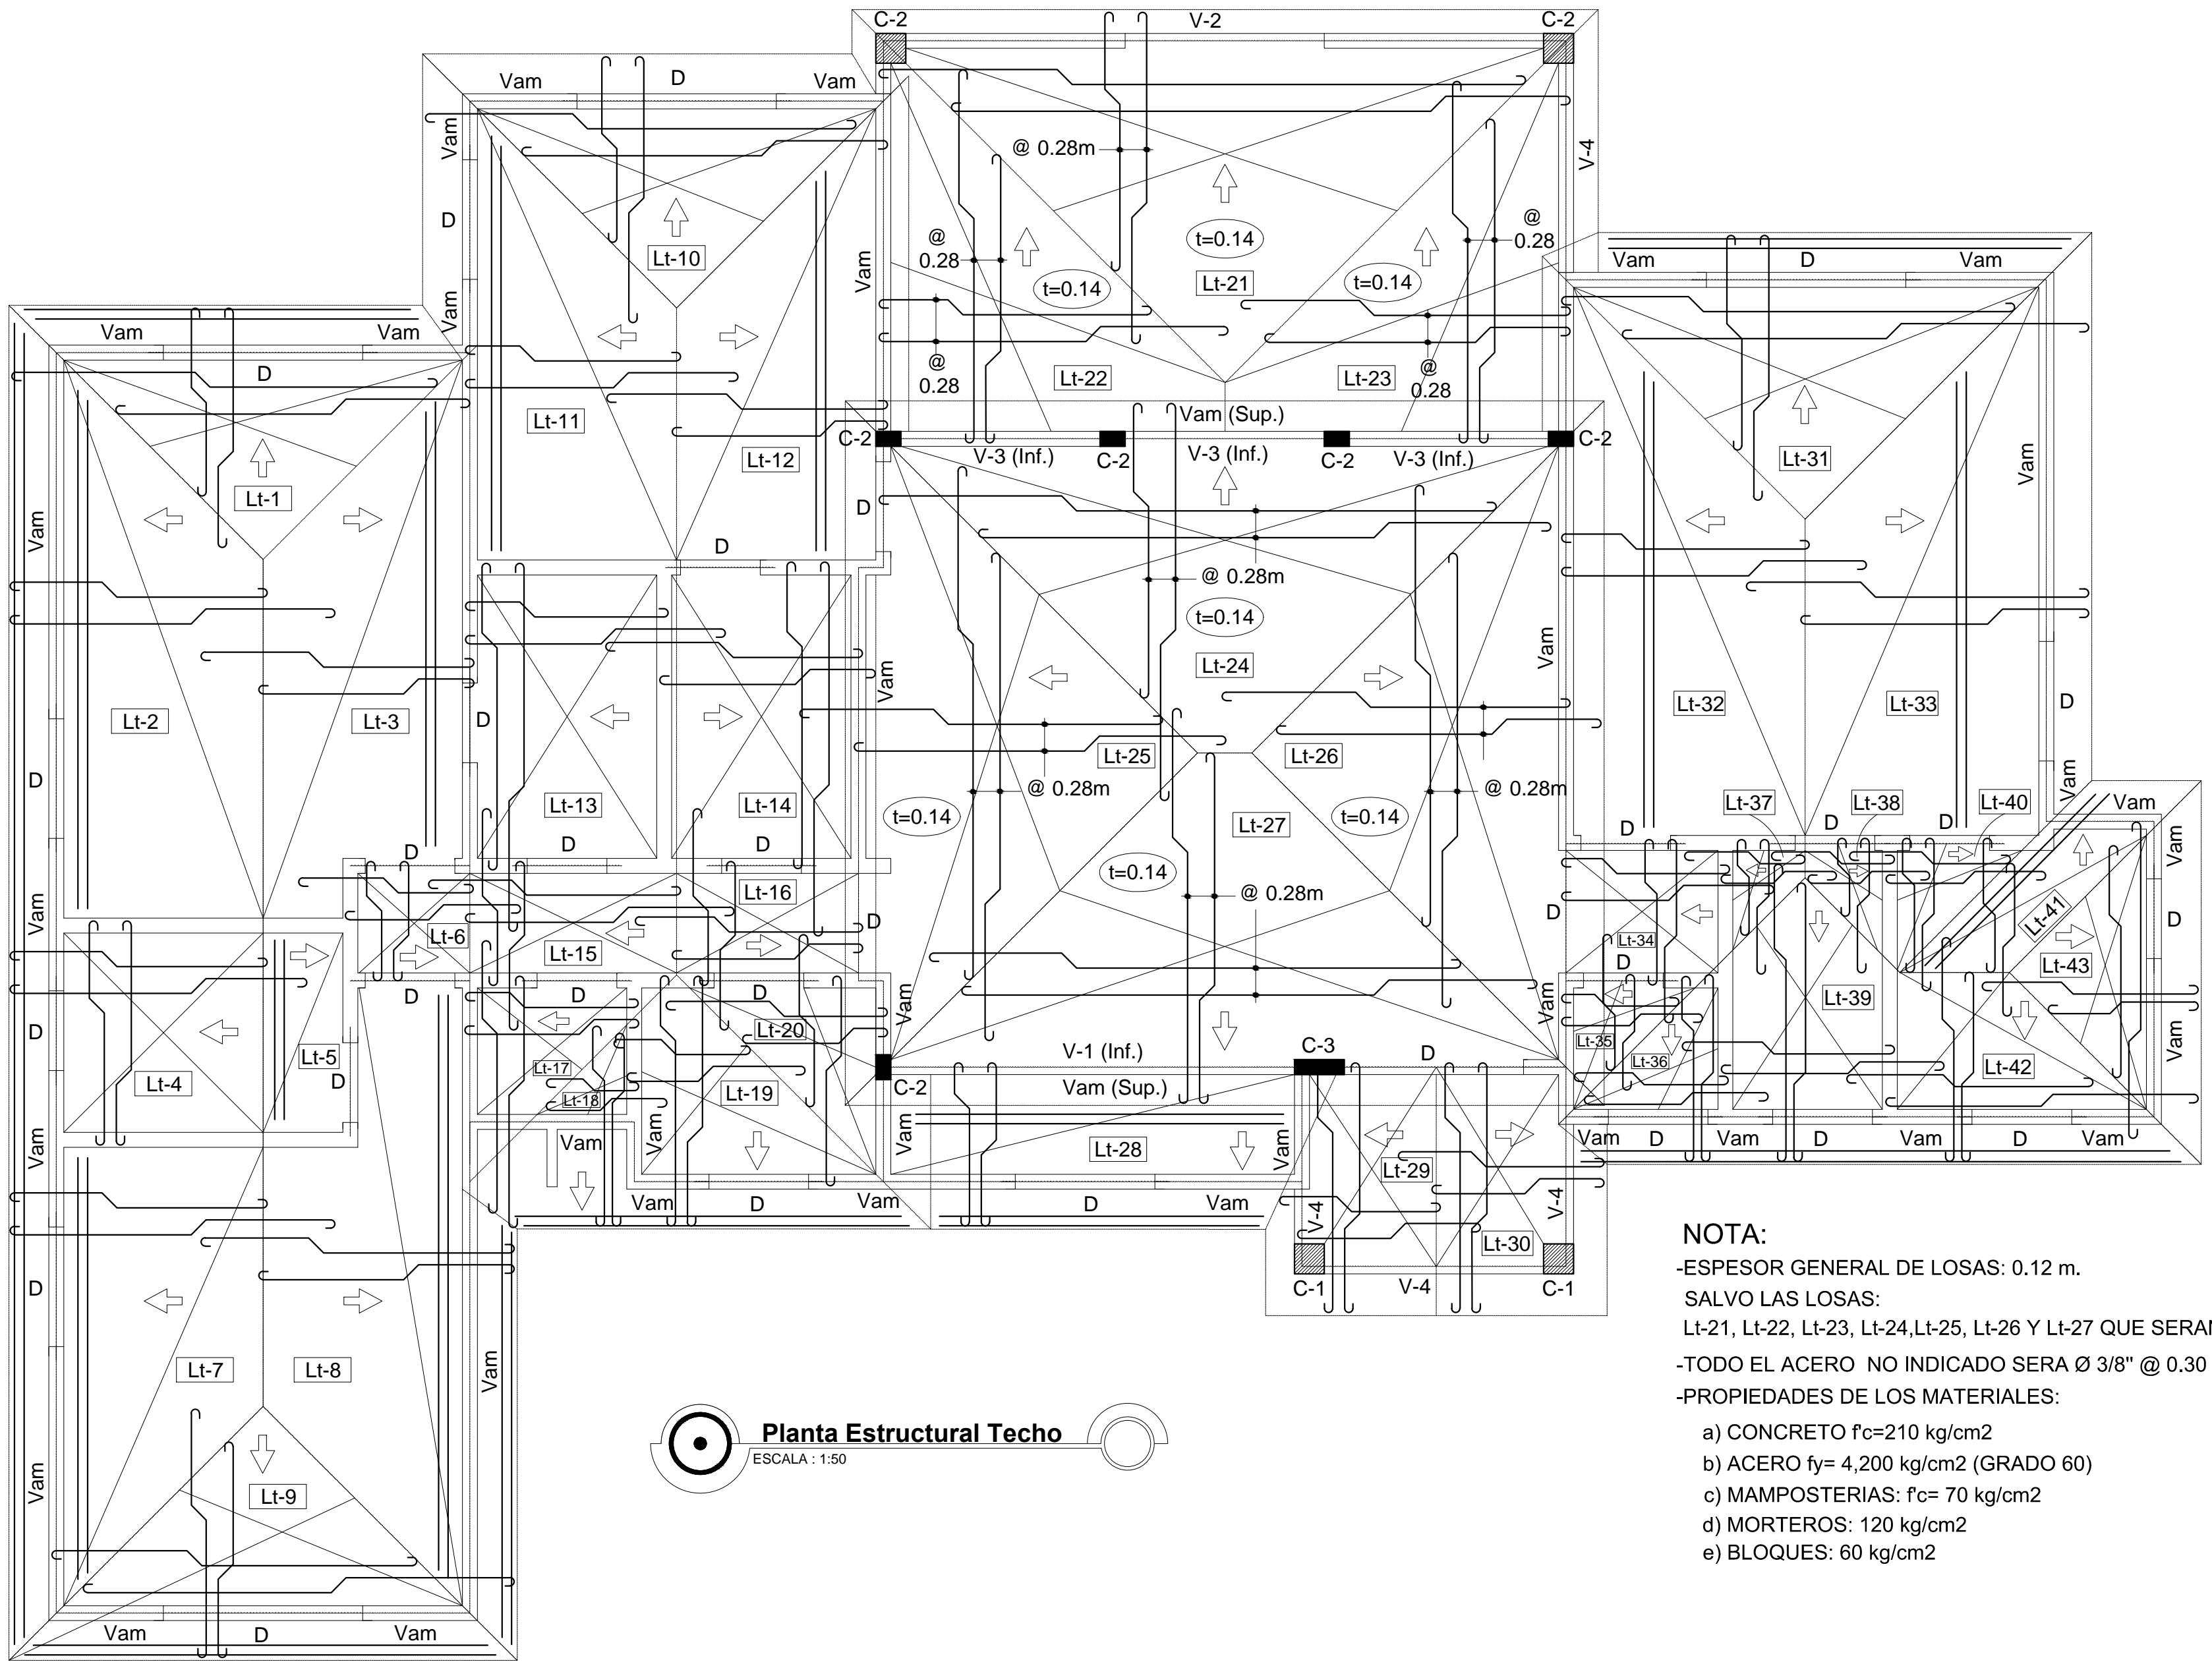


## TECHO

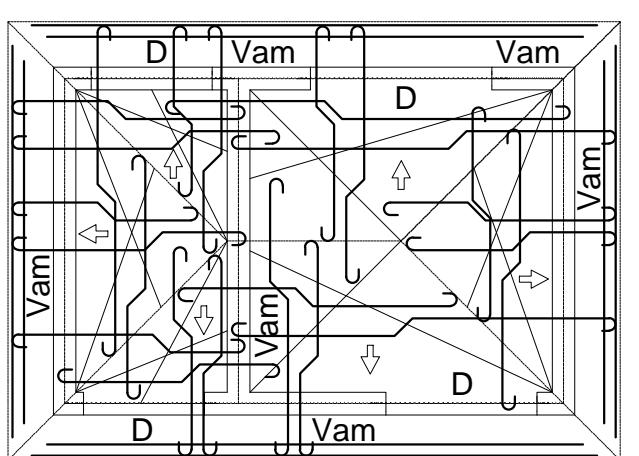


NOTA:  
-ESPESOR GENERAL DE LOSAS: 0.10 m.  
-TODO EL ACERO NO INDICADO SERA Ø 3/8" @ 030 m

## FUNDACIONES

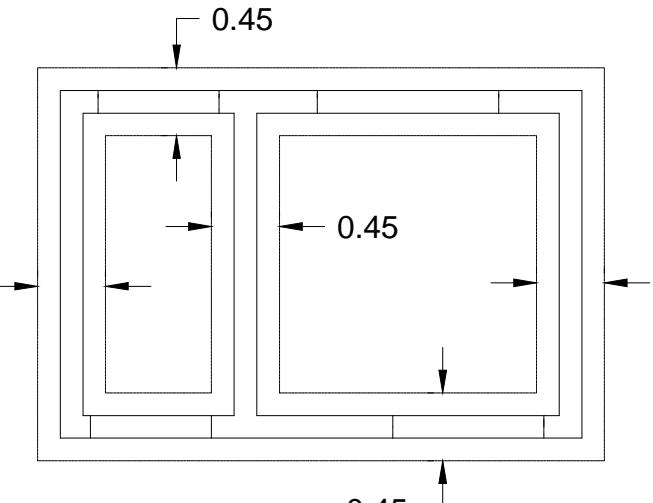


## DETALLE REFUERZO VERTICAL EN LAS INTERSECCIONES DE LOS MUROS


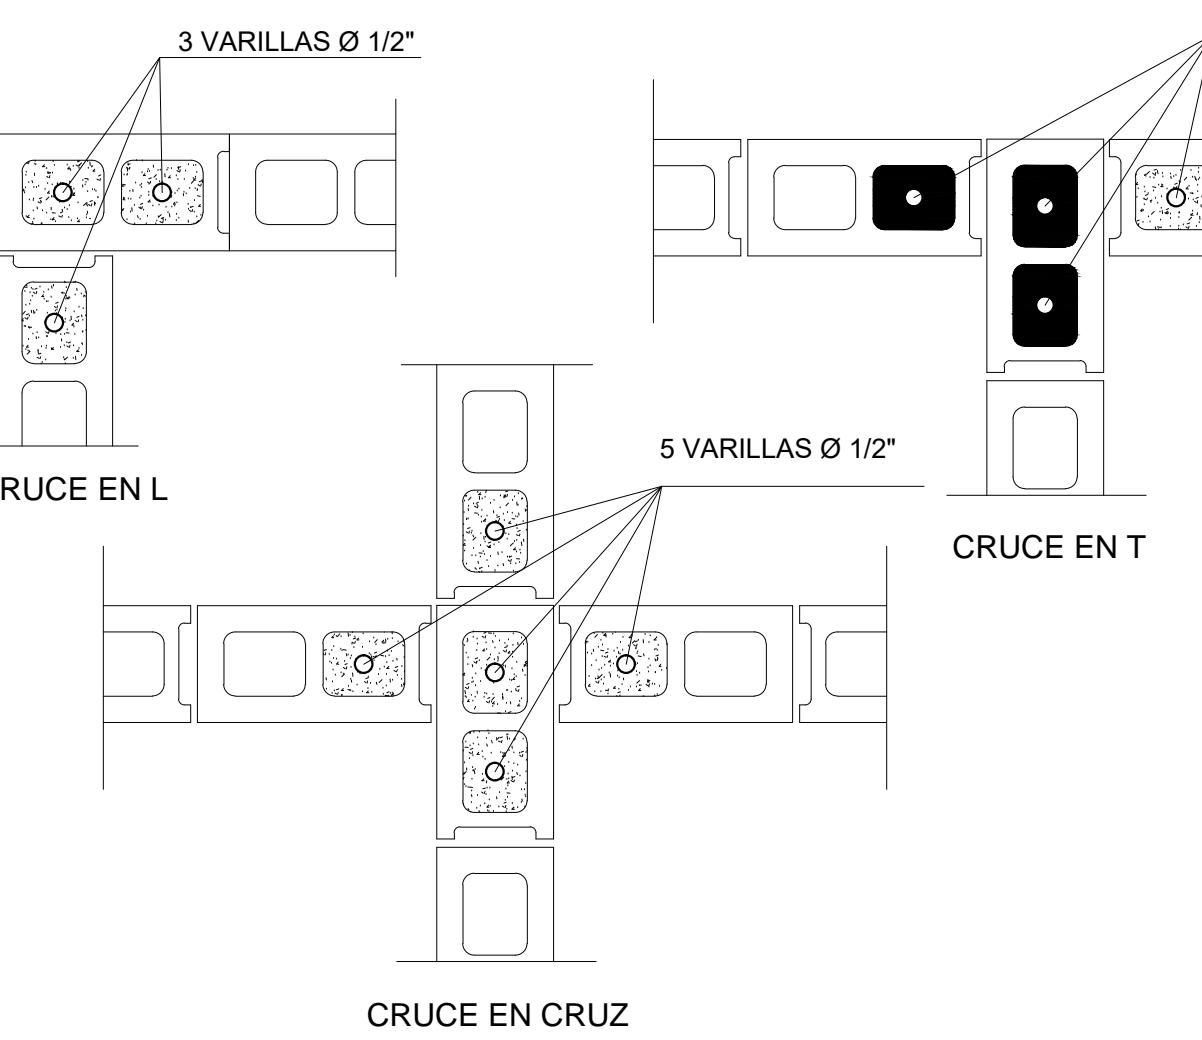


CRUCE EN CRUZ


## DETALLES DE VIGAS :

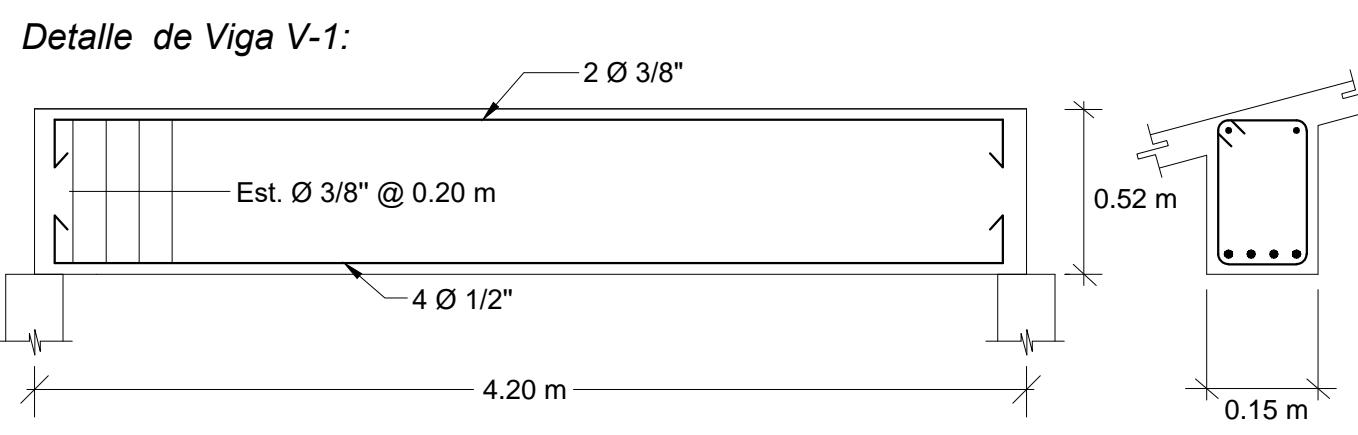



## DETALLE DINTEL D :

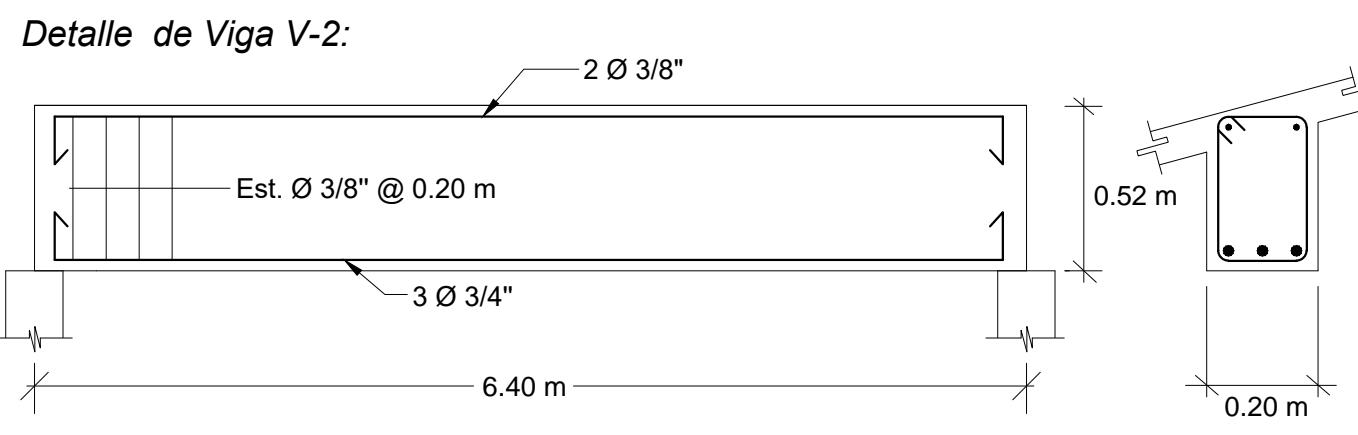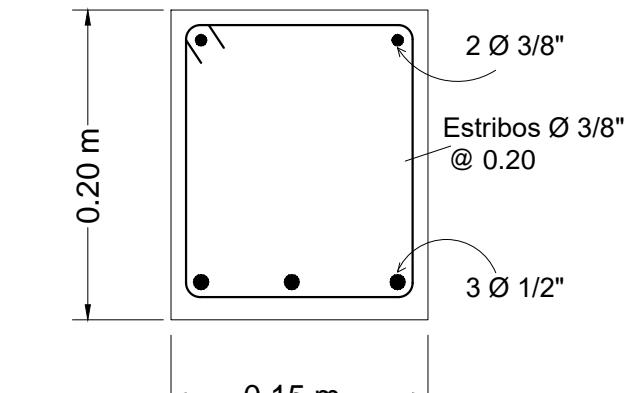

## DET. VIGA AMARRE VAM :

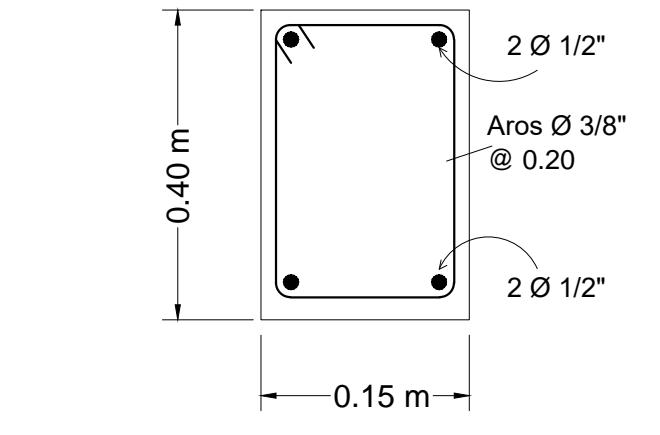

Colocar a no más de 15 líneas de separación vertical

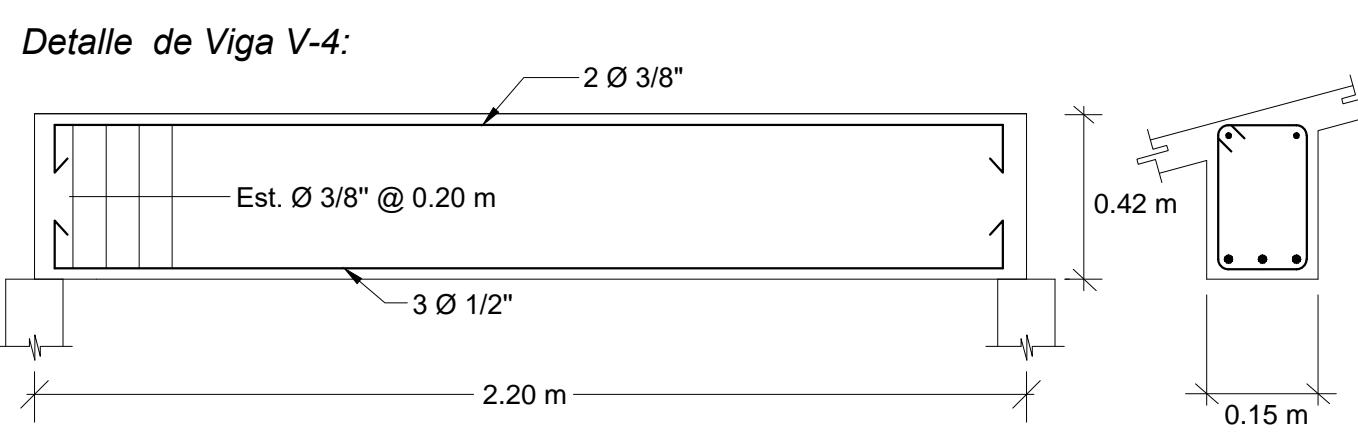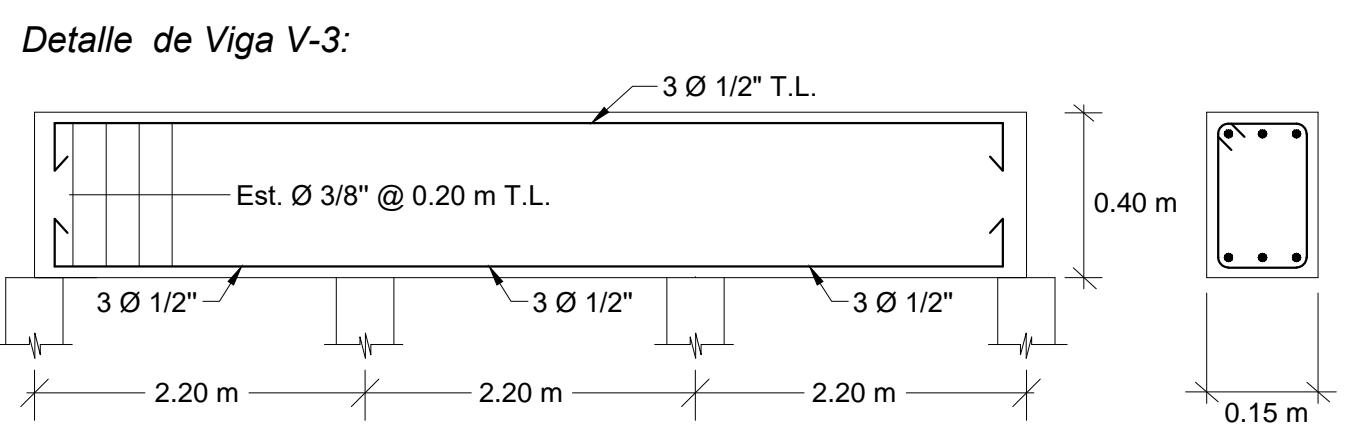


## NOTA:

-ESPESOR GENERAL DE LOSAS: 0.12 m.  
SALVO LAS LOSAS:  
Lt-21, Lt-22, Lt-23, Lt-24, Lt-25, Lt-26 Y Lt-27 QUE SERAN t = 014m. REFUERZOS EN ABERTURAS EN MUROS DE BLOQUES

-TODO EL ACERO NO INDICADO SERA Ø 3/8" @ 0.30 m


-PROPIEDADES DE LOS MATERIALES:

- CONCRETO  $f_c=210 \text{ kg/cm}^2$
- ACERO  $f_y= 4,200 \text{ kg/cm}^2$  (GRADO 60)
- MAMPOSTERIAS:  $f_c= 70 \text{ kg/cm}^2$
- MORTEROS:  $120 \text{ kg/cm}^2$
- BLOQUES:  $60 \text{ kg/cm}^2$

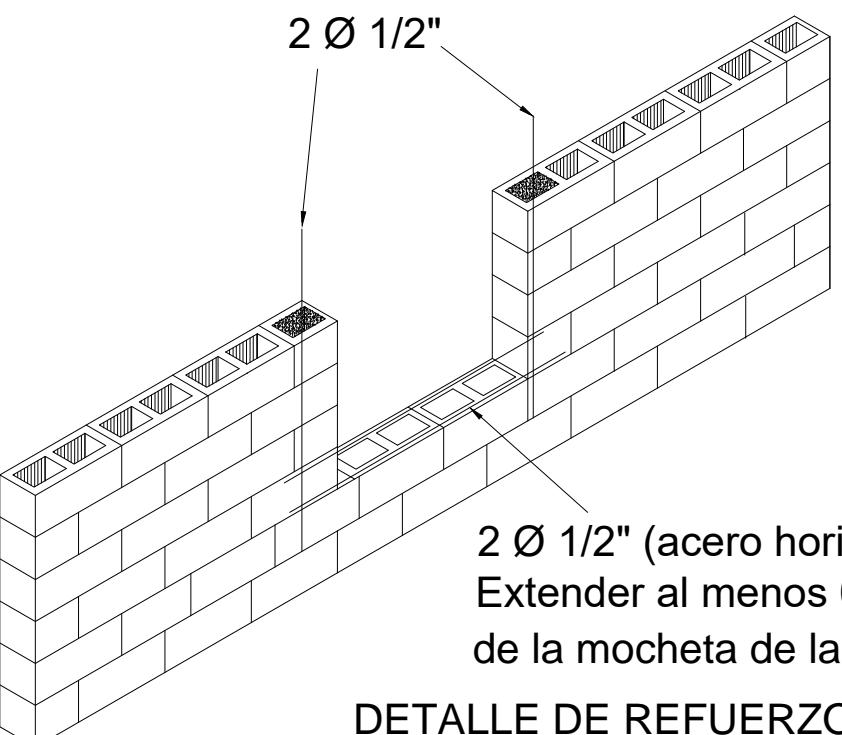


2 Ø 1/2" (acero horizontal)  
Extender al menos 0.40 más allá  
de la mocheta de la ventana .


## DETALLE DE REFUERZO HORIZONTAL EN LAS INTERSECCIONES DE MUROS:

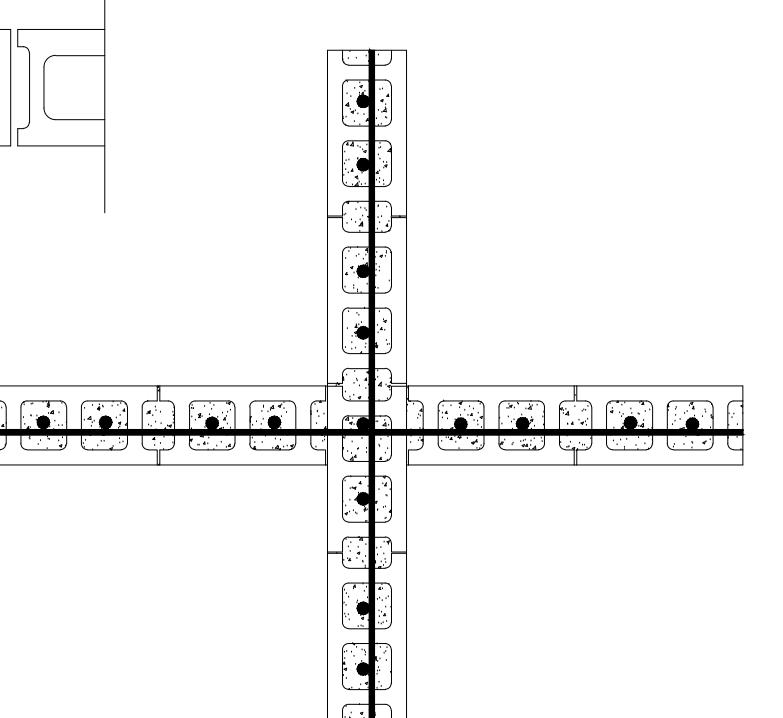

## Extremos de Muros

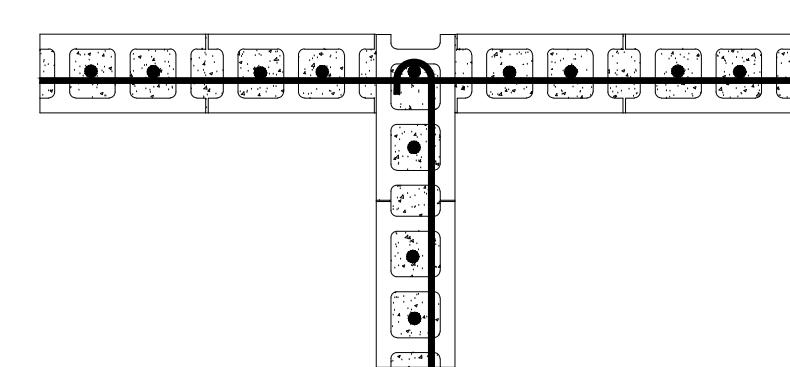

## Cruces en T

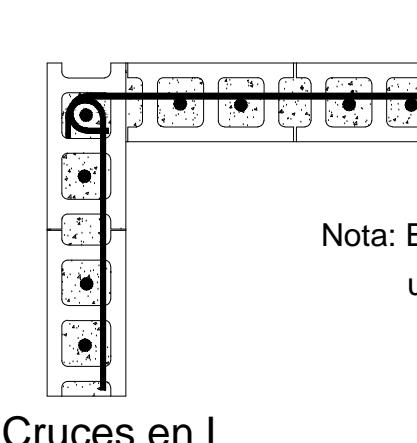

Nota: En algunos casos solo se muestra  
una serpentina por claridad del dibujo.

## Ficha Técnica


No.	Descripción	Fecha
DIS. ARQUITECTONICO	CODIA	
ARQ. ERIS ESPINAL	19346	CODIA
DIS. ESTRUCTURAL		
ING. JOAQUIN BOLIVAR ALMANZAR	8608	CODIA
DIS. ELECTRICO		
ING. HECTOR HERNANDEZ	18559	CODIA
DIS. SANITARIO		
ARQ. ERIS ESPINAL	19346	CODIA
DIGITACION		
ARQ. ESTEBAN DEOGRAZIA	37644	CODIA
COORDINACION Y REVISION		
ARQ. ESTEBAN DEOGRAZIA	37644	CODIA
RESPONSABLE DEL PROYECTO		

## PROYECTO


Casa Yuri y Marina

UBICADO EN: Sosua- Cabarete Sosua Ocean Village	
CONTENIDO :	Plano Estruct. de Techo + Detalles
PROPIETARIO :	
REFERENCIA DE PLANOS :	Plano Terminado
FECHA :	Marzo/2020
No. De Hojas.	
ESCALA: Indicada	7
	11


### DIAGRAMA UNIFILAR

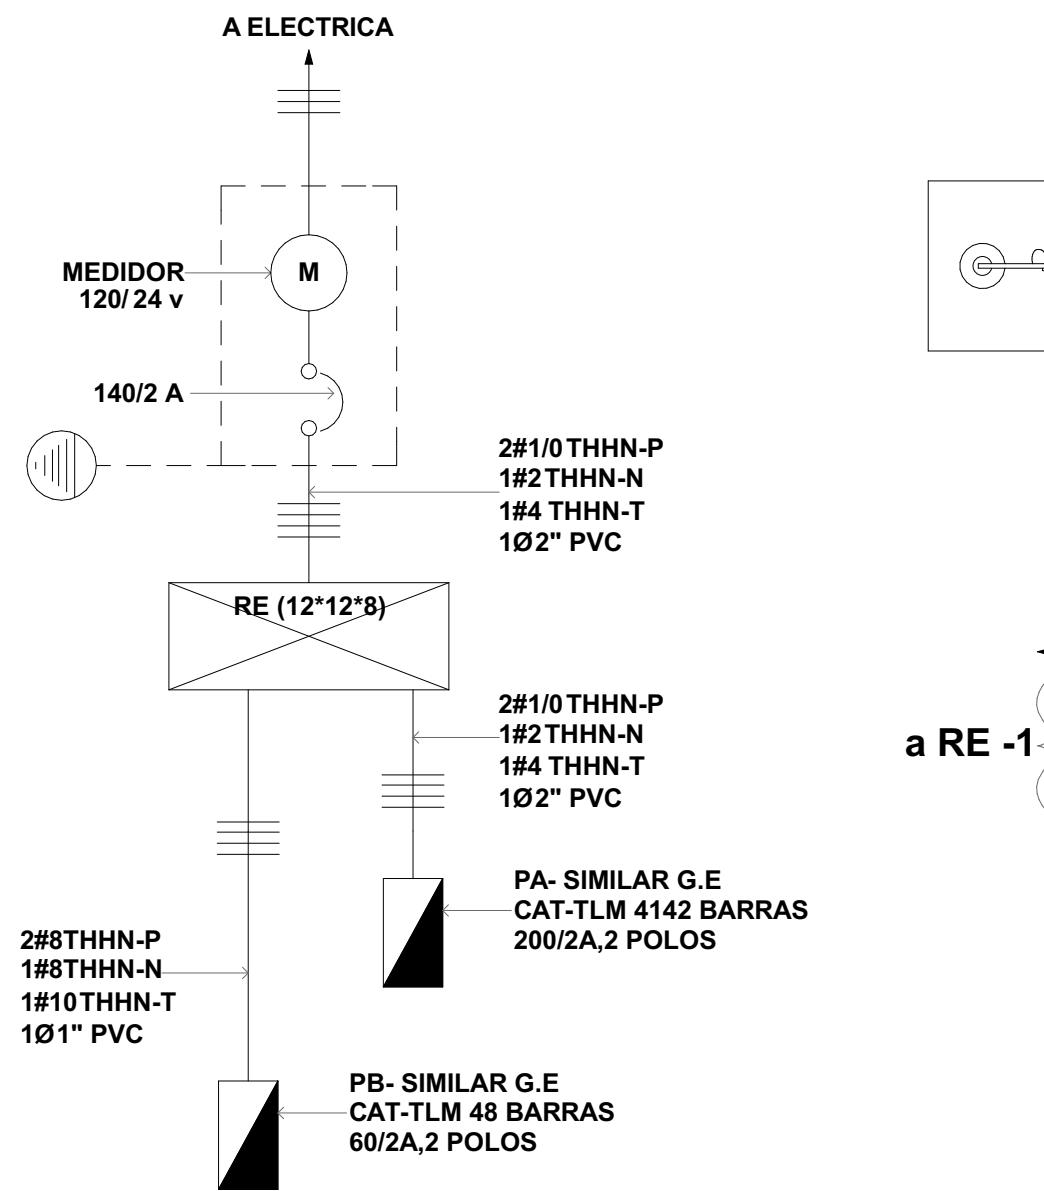

### DETALLE DE CUARTO DE BOMBAS

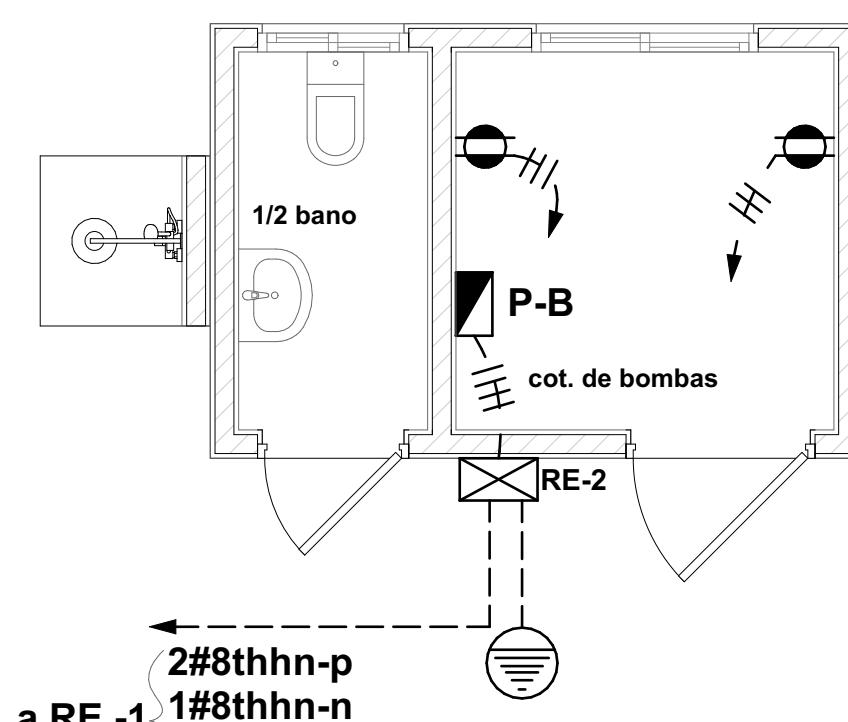

### DIAGRAMA DE ALIMENTACION Y DRENAJE PARA A/ACOND. SPLIT

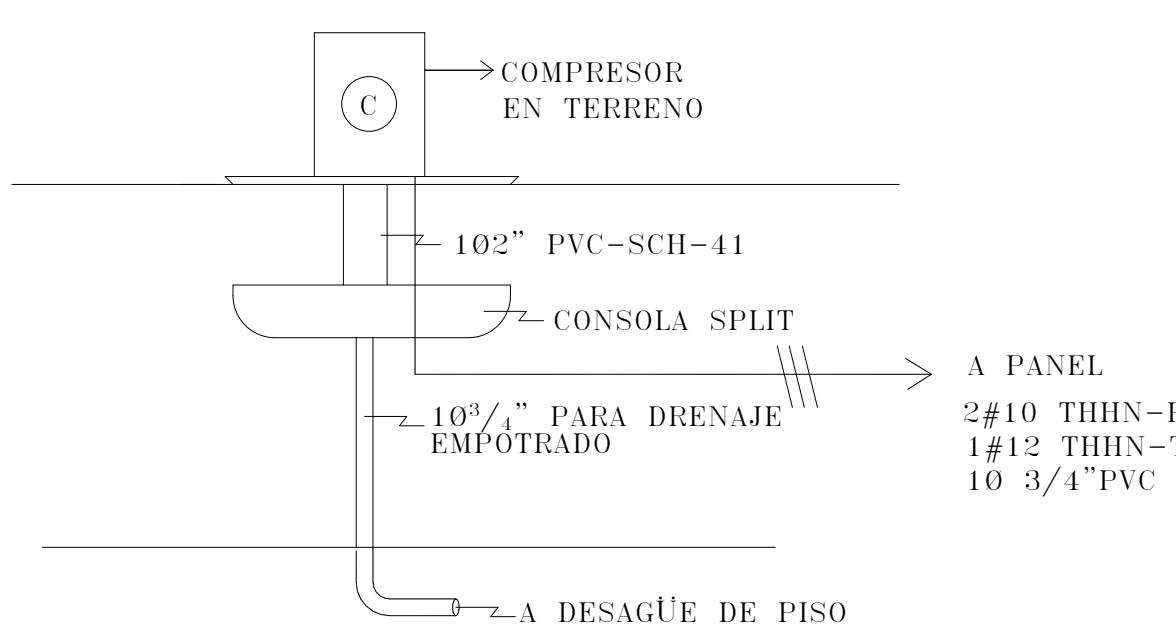

Nota: todos los ductos utilizados en las instalaciones electricas seran del tipo PVC DR. 26 S.I.C.

### TABLA DE CODIGO DE COLORES


COLOR	DESCRIPCION
NEGROS	POTENCIALES
BLANCOS	NEUTROS
AZUL	RETORNOS
VERDE	TIERRA

NOTA> TODOS LOS CONDUCTORES PROPOSTOS SERAN DEL TIPO THHN Y LOS DUCTOS SERAN DEL TIPO SDR-26-S.I.C.


a terreno  
102" pvc y  
drenaje de  
10 3/4" pvc

TERRAZA

a terreno  
102" pvc y  
drenaje de  
10 3/4" pvc

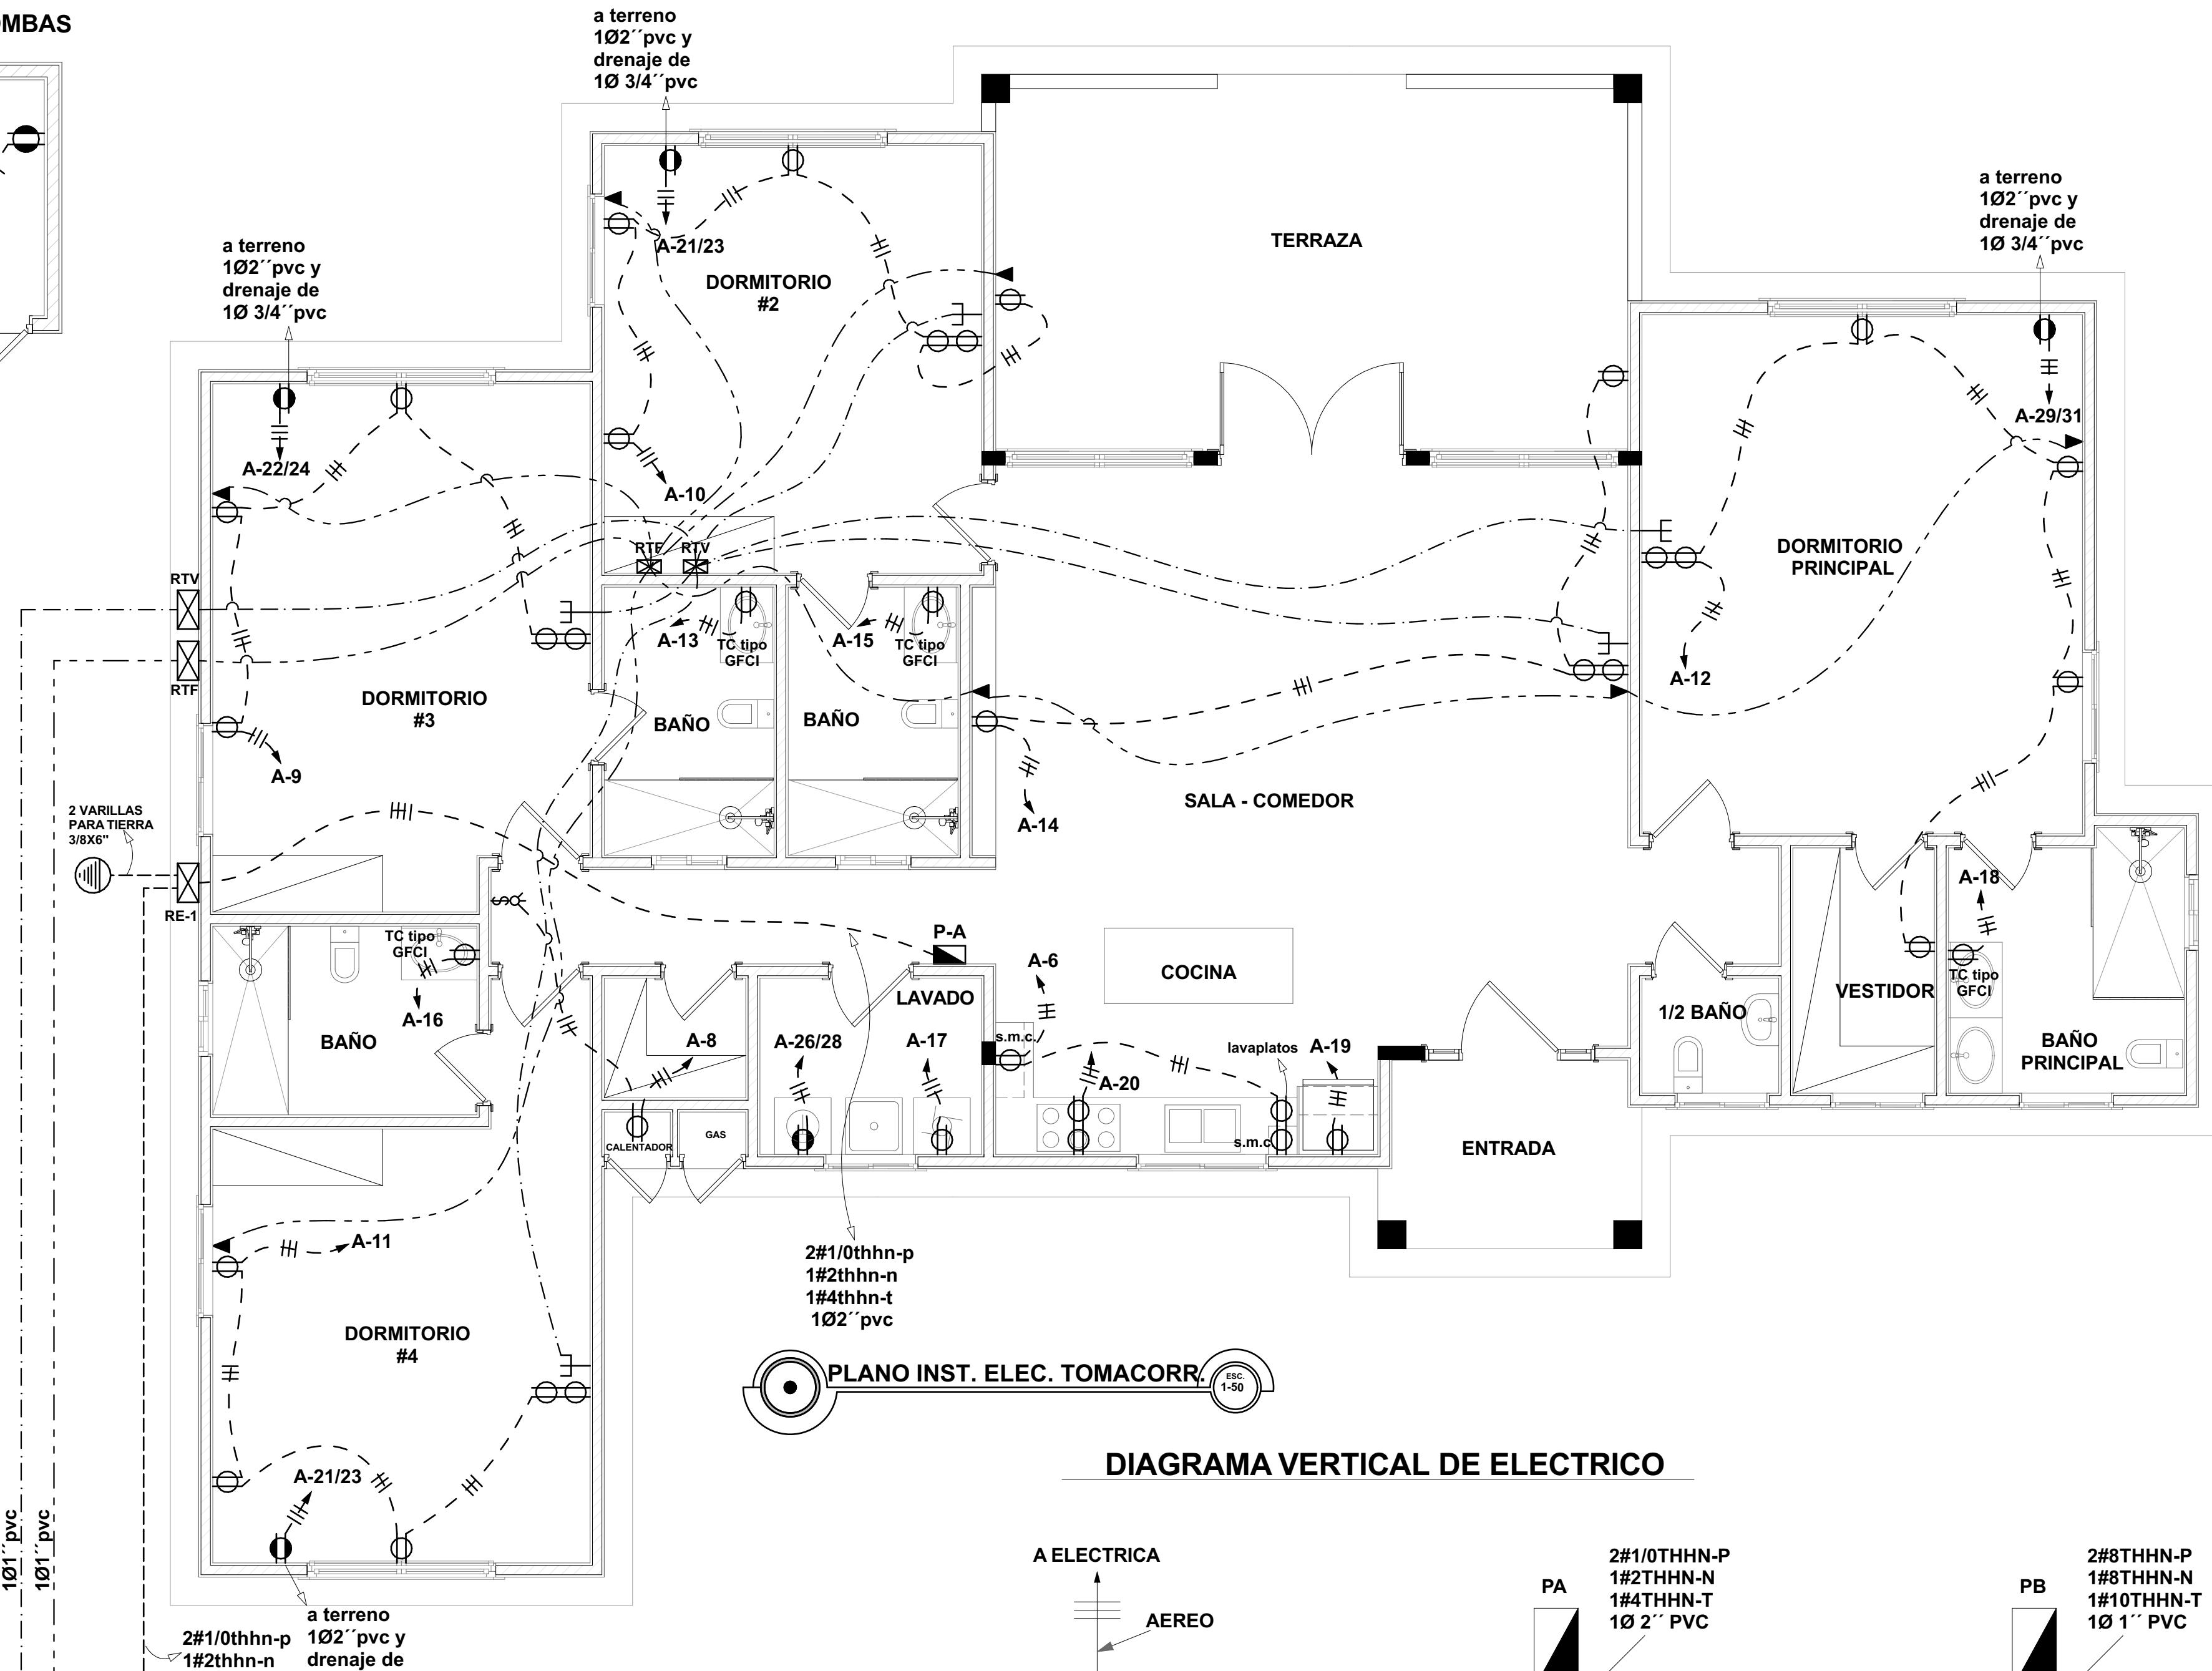

### DIAGRAMA VERTICAL DE ELECTRICO

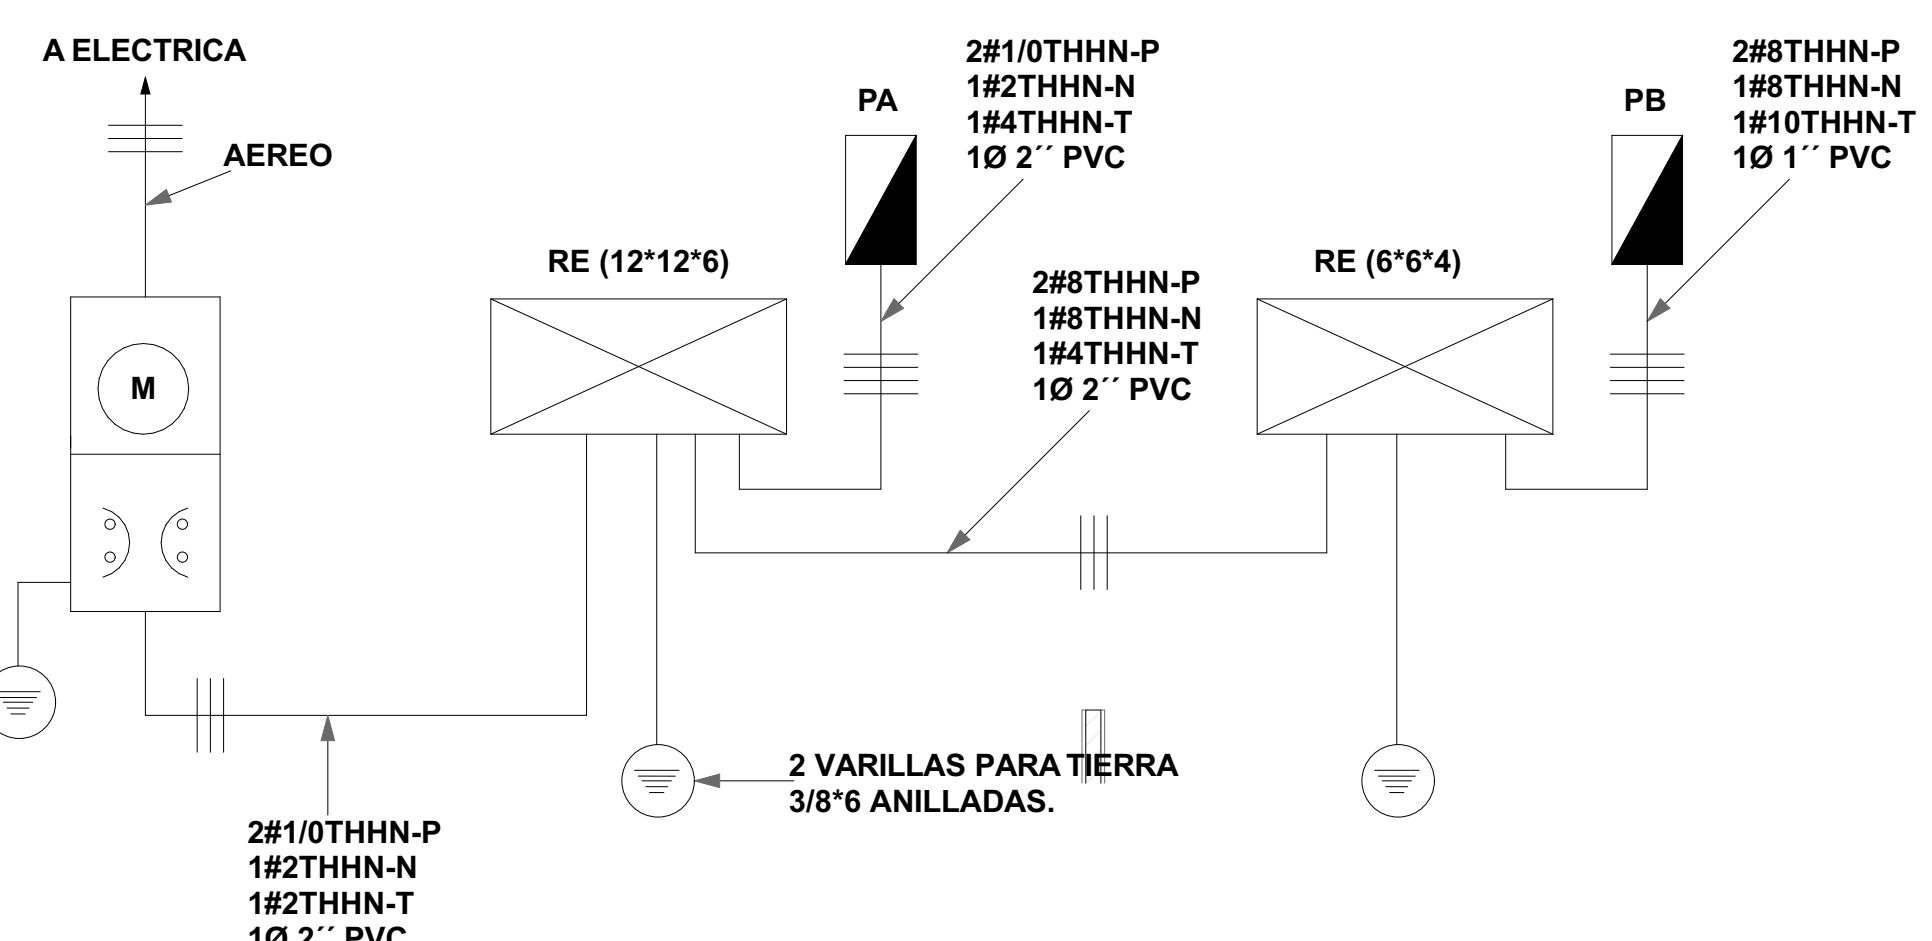

### DETALLE DE PISCINA





3- Las luces de piscina seran del tipo LED-18watts y estaran gobernadas todas por un transformador de 75w 120v\_12v\_150watts ubicado caseta de bombas.

No.	Descripción	Fecha
-----	-------------	-------




### Ficha Técnica

1.SL. ARQUITECTONICO	COOPA
ARQ. ERIS ESPINAL	19346
ING. JOAQUIN BOLIVAR ALMANZAR	8608
ING. ESTEBAN DEGRACIA	18559
ING. HECTOR HERNANDEZ	18559
1.SL. SANITARIO	COOPA
ARQ. ERIS ESPINAL	19346
2.GITACION	COOPA
ARQ. ESTEBAN DEGRACIA	37644
2.GITACION	COOPA
ARQ. ESTEBAN DEGRACIA	37644
3.ORDENES DEL PROYECTO	COOPA
PROYECTO	Casa Yuri y Marina
UBICADO EN:	Sosua - Cabarete Sosua Ocean Village
CONTENIDO :	Plano Inst. Elect. Tomacorr. + Detalles
PROPIETARIO :	
REFERENCIA DE PLANOS :	Plano Terminado
FECHA :	Marzo/2020
No. De Hojas.	8
ESCALA:	Indicada
	11

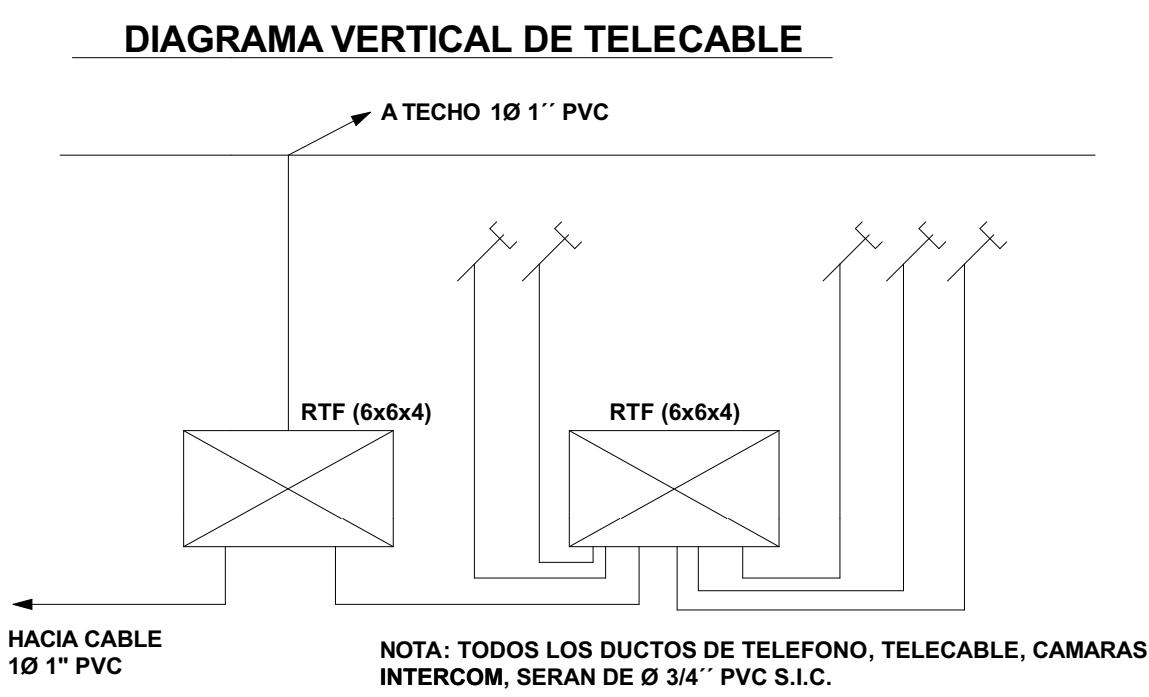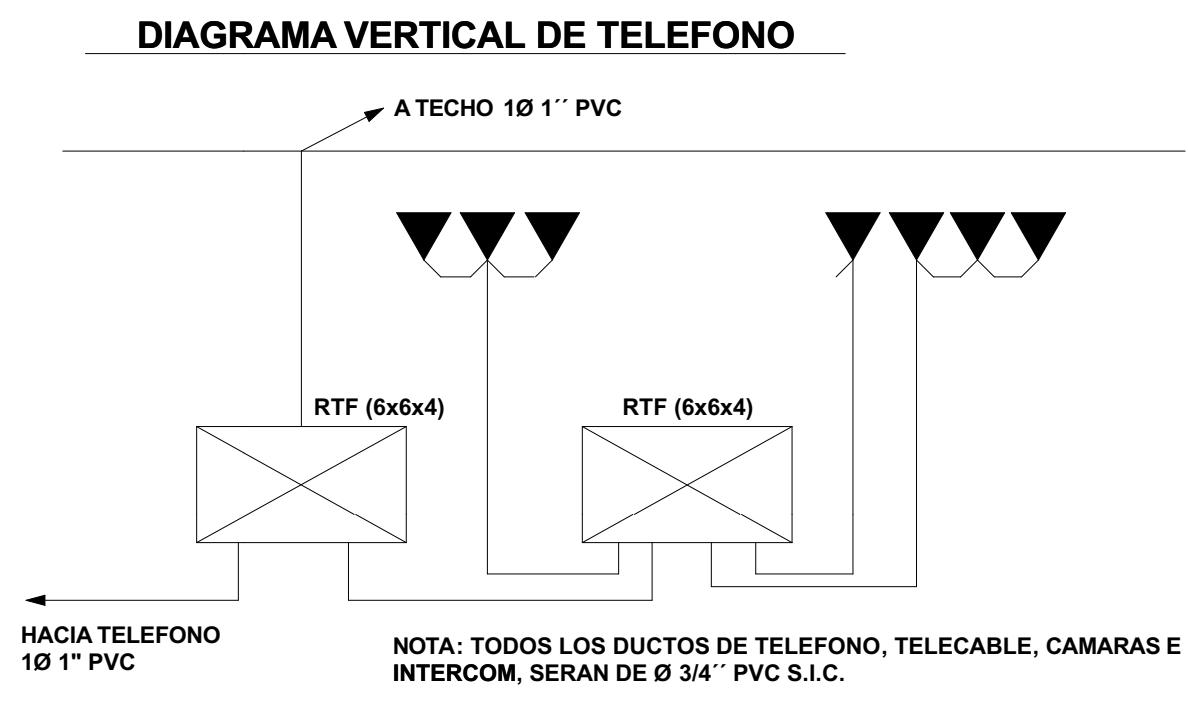

# Leyenda

	luces piscina propuestro
	Transformador luces de piscina
	Transformador PAD mounted propuestro
	Luminaria de Techo
	Luminaria de Pared
	Abanico de Techo
	Interruptor Sencillo @ 1.20 Mt. SNPT
	Interruptor Doble @ 1.20 Mt. SNPT
	Interruptor Triple @ 1.20 Mt. SNPT
	Interruptor Three Way @ 1.20 Mt. SNPT
	Interruptor con Luz Piloto
	Pulsador de Timbre
	Tomacorrientes 120 Voltios @ 0.40 SNPT
	Tomacorrientes 220 Voltios
	Salida Teléfono @ 0.40 SNPT
	Salida de Televisión (Cable) @ 0.40 Mt.
	Registro Eléctrico @ 0.40 Mt SNPT
	Registro Teléfono @ 0.40 Mt SNPT
	Registro Cable / TV @ 0.40 Mt SNPT
	Registro Intercom @ 0.40 Mt SNPT
	Panel de Distribución @ 1.60M SNPT
	Poste Existente
	Para Rayo
	Cut-Out
	Cono de Alivio
	Transformador PAD mounted diagrama unifilar
	Camaras
	Bocinas
	Intercom Interior
	Intercom Exterior
	Varilla Puesta Tierra
	Tubería que Sube o Baja Empotrada
	Tubería Empotrada en Techo
	Tubería Empotrada en Piso
	Línea Hacia Panel de Distribución
	Línea Telefónica
	Línea Televisión
	Línea de Timbre

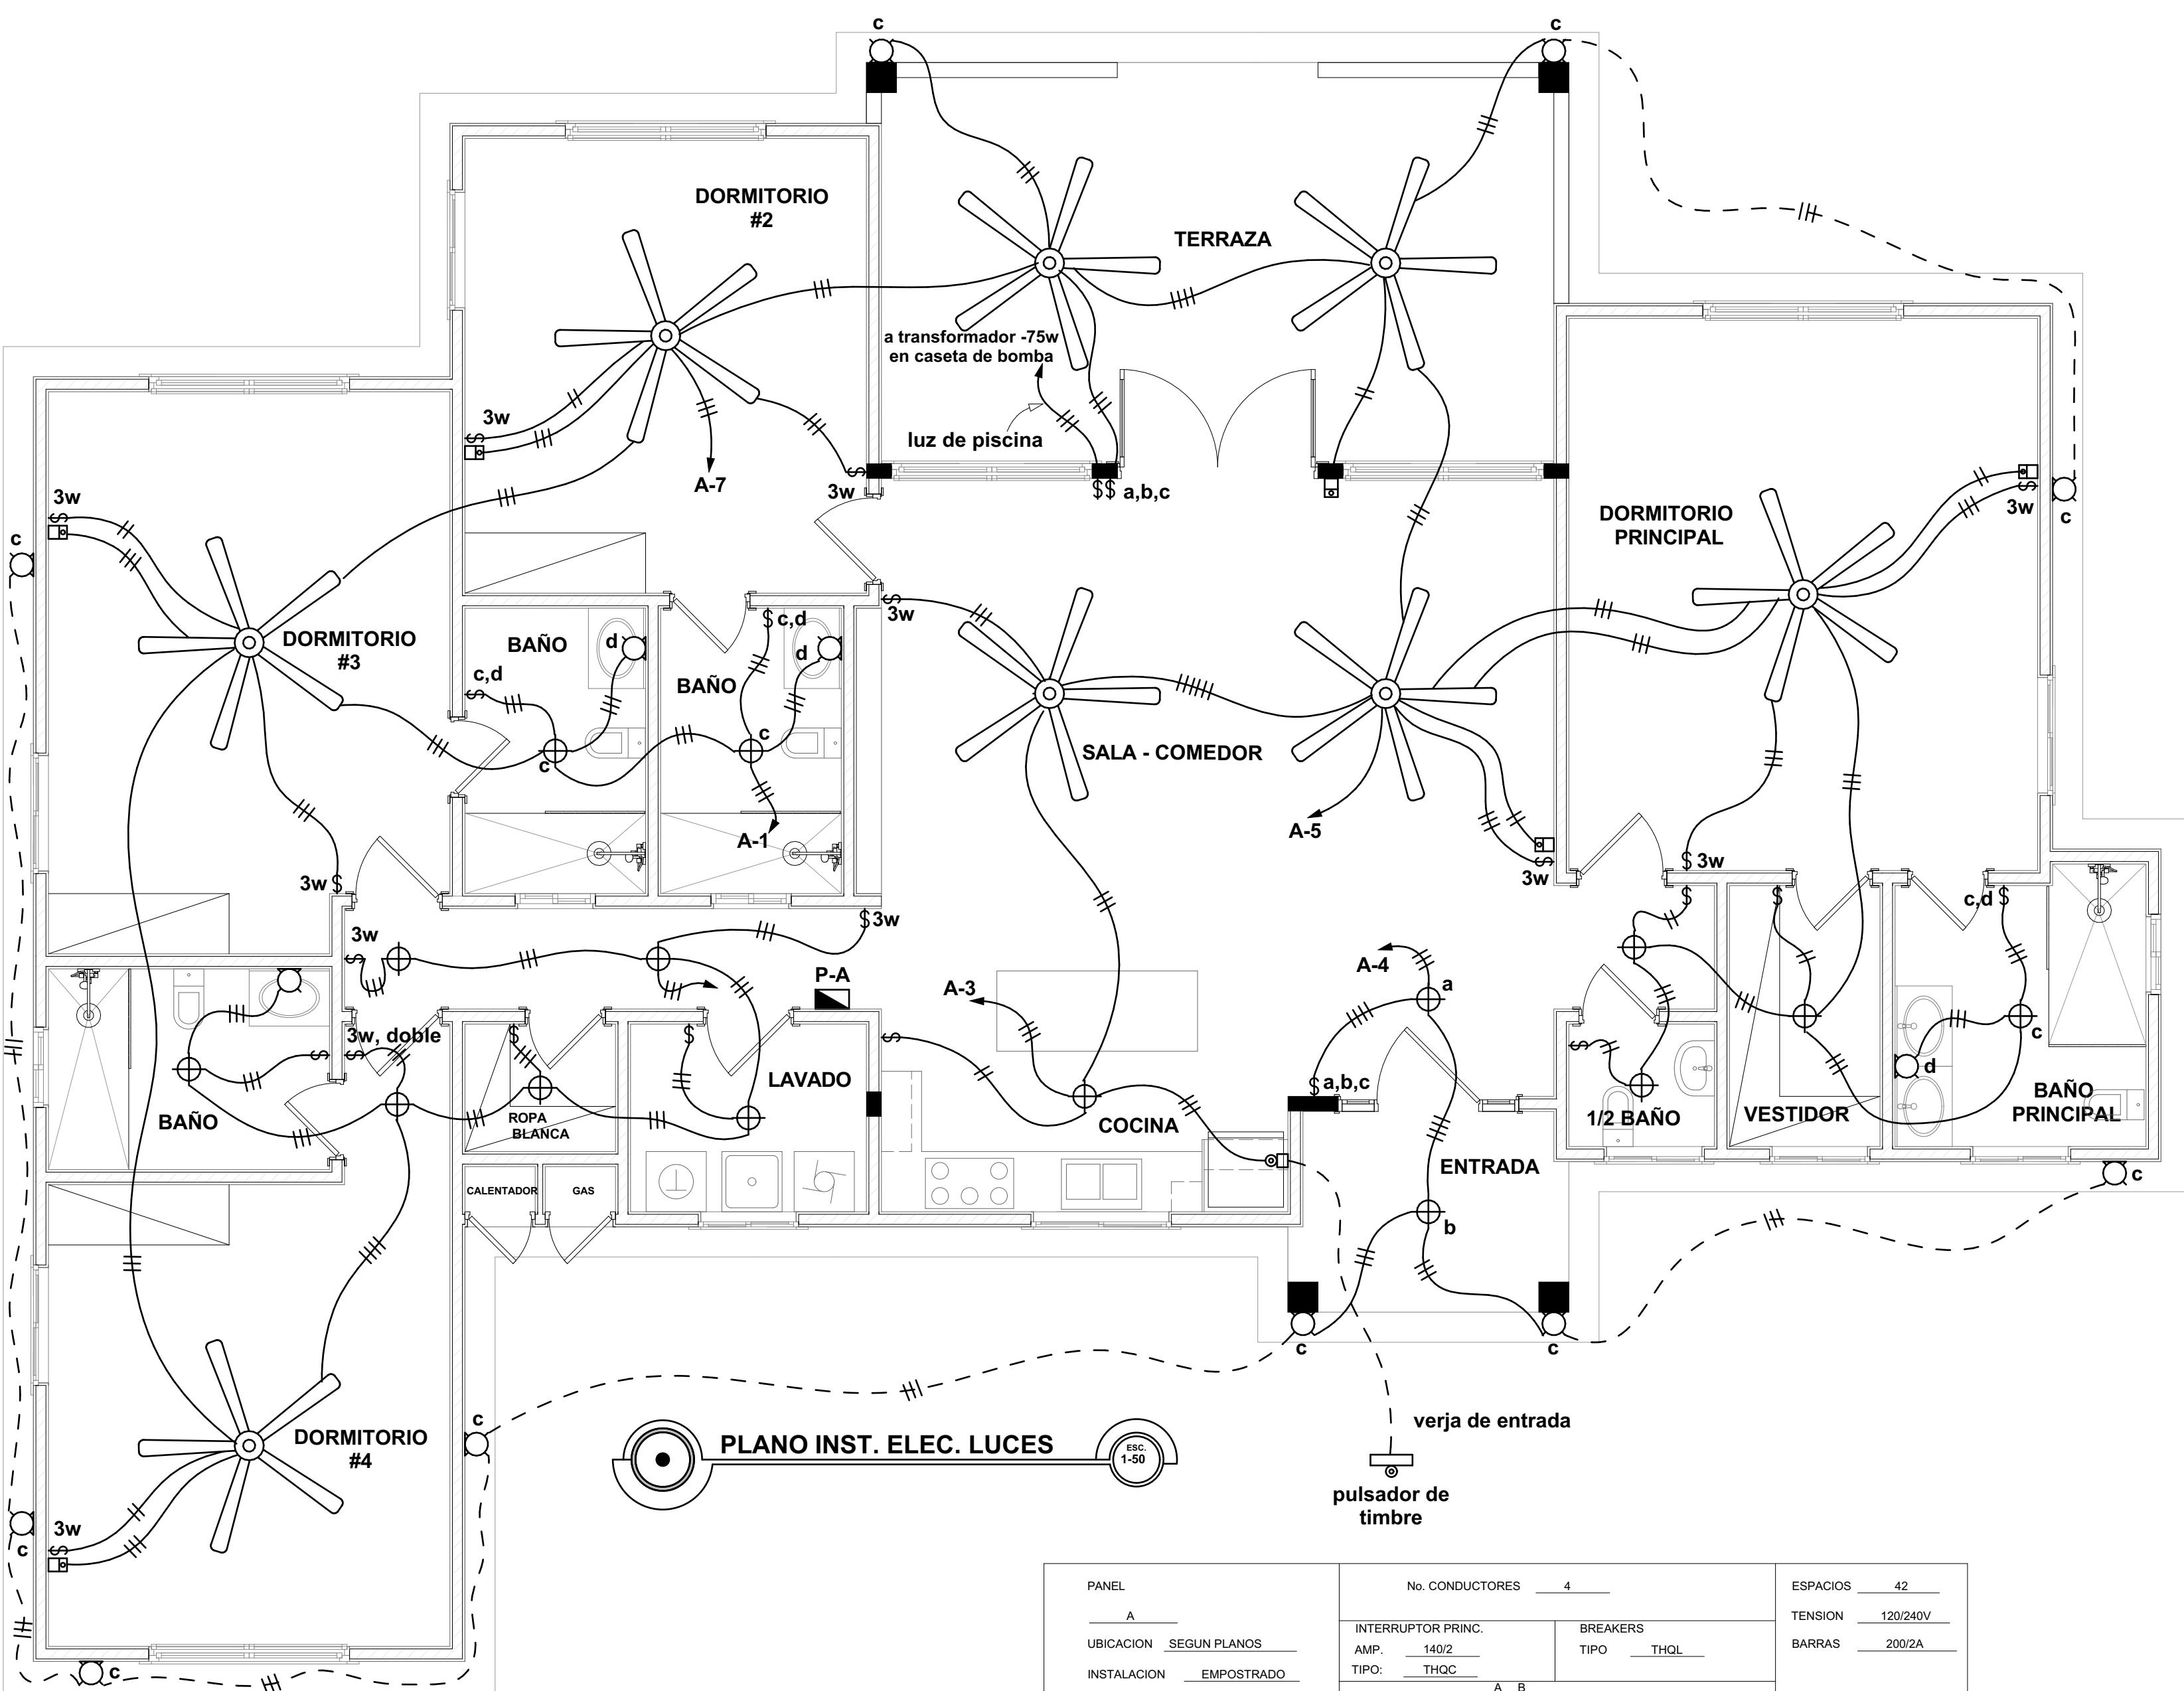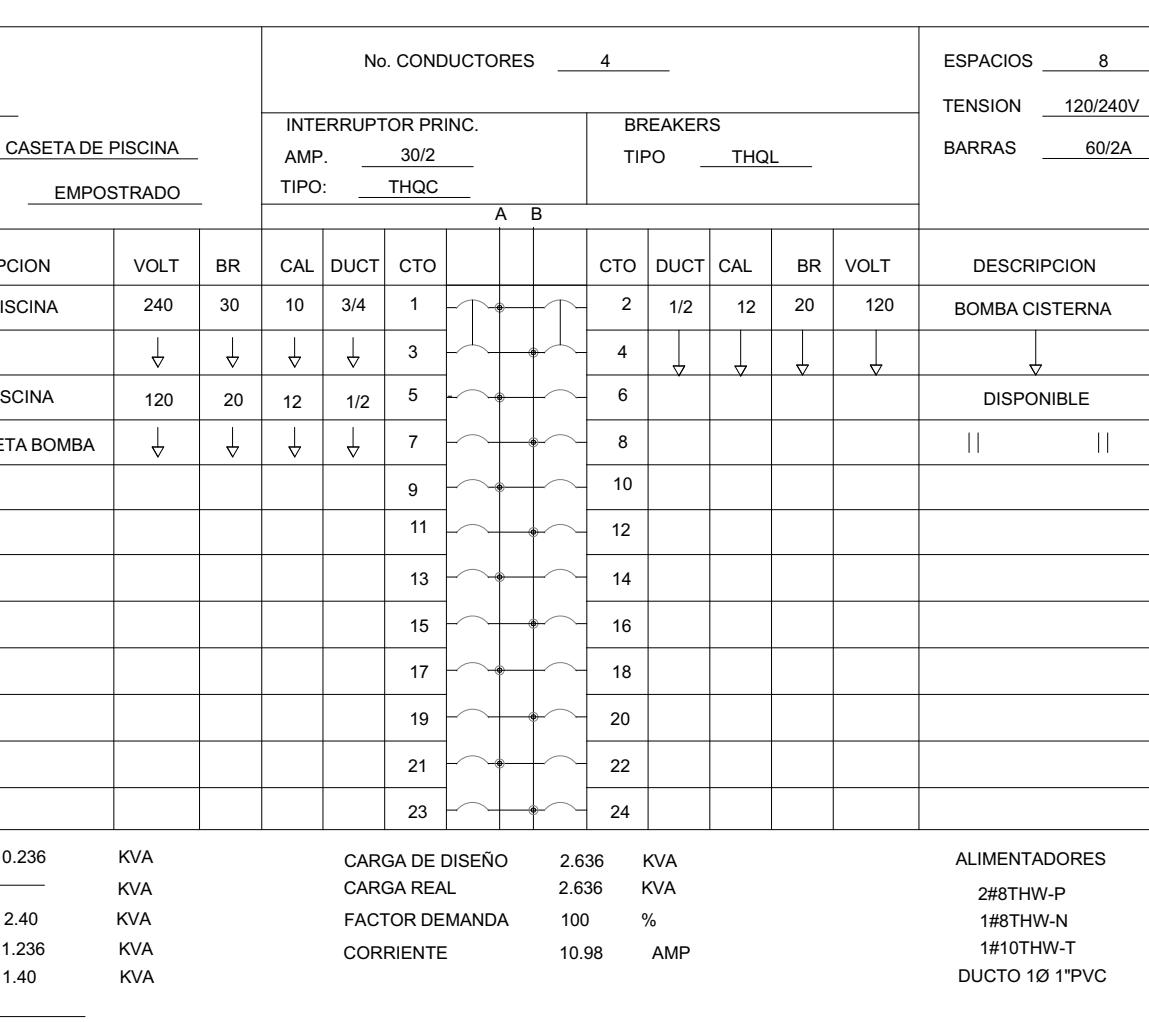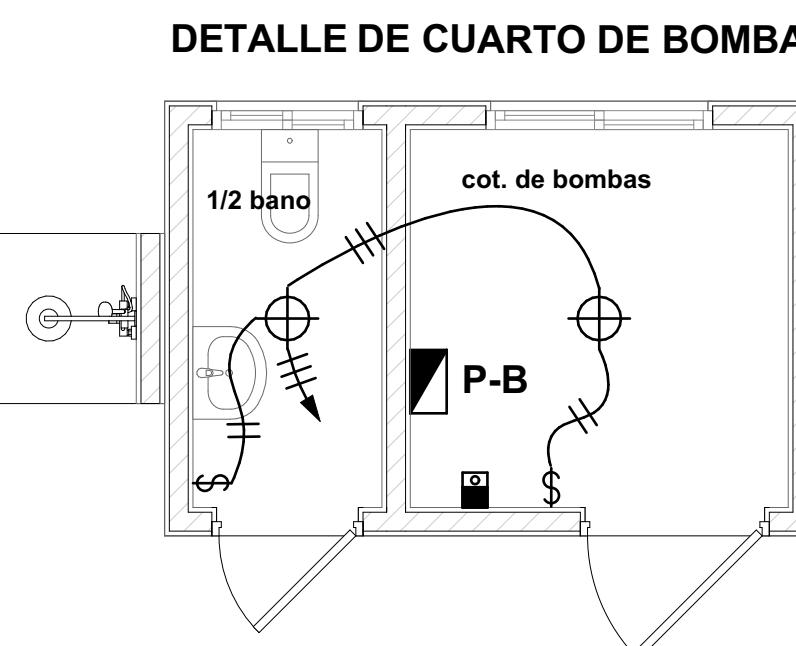

# **Ficha Técnica**

DIS. ARQUITECTONICO	CODIA
ARQ. ERIS ESPINAL	19346
DIS. ESTRUCTURAL	CODIA
ING. JOAQUIN BOLIVAR ALMANZAR	8608
DIS. ELECTRICO	CODIA
ING. HECTOR HERNANDEZ	18559
DIS. SANITARIO	CODIA
ARQ. ERIS ESPINAL	19346
DIGITACION	CODIA
ARQ. ESTEBAN DEOGRAZIA	37644
COORDINACION Y REVISION	CODIA
ARQ. ESTEBAN DEOGRAZIA	37644
RESPONSABLE DEL PROYECTO	CODIA

## PROYECTO **Casa Yuri y Marina**

**UBICADO EN: Sosua- Cabarete**

**CONTENIDO :**

**Paso Inst. Elect. Luces + Detalles**

PROPIETARIO :

## **REFERENCIA DE PLANOS :**

FECHA : No. De Hojas.

**ESCALA: Indicada**




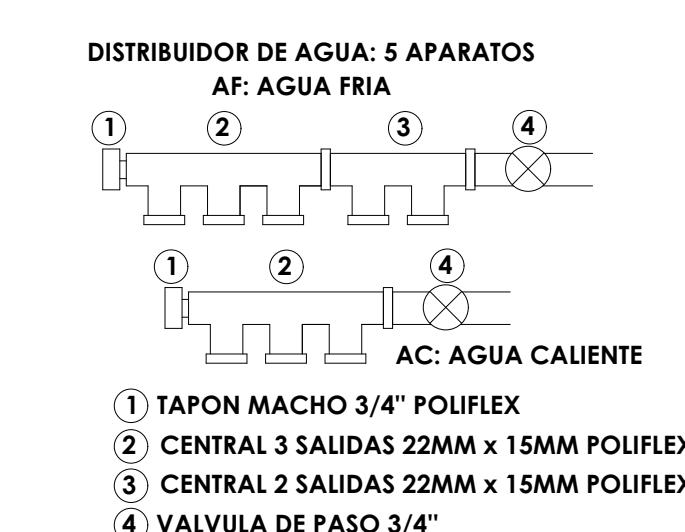


TABLA GENERAL DE SIMBOLOS	
—	Tub. A.F. pvc sch-40
-----	Tub. A.C. cpvc sch-40
Lv	Lavabo
Du	Ducha
Ba	Bañera
Ic	Inodoro con cisterna
Fr	Fregadero de cocina
La	Lavadora
Ld	Lavadero
Gf	Grifo
Llj	Llave de jardín
→	Consumos
●	Llave de paso
~	Válvula de retención
●	Calentador
⊗	Llaves generales
●	Bombas
●	Tanque Hidroneumático
□	Cisterna
■	Contador

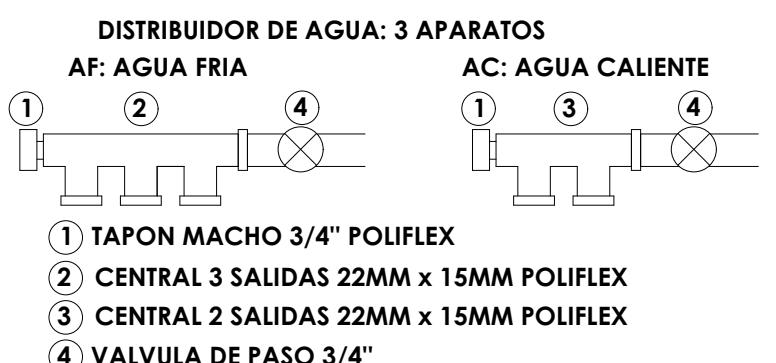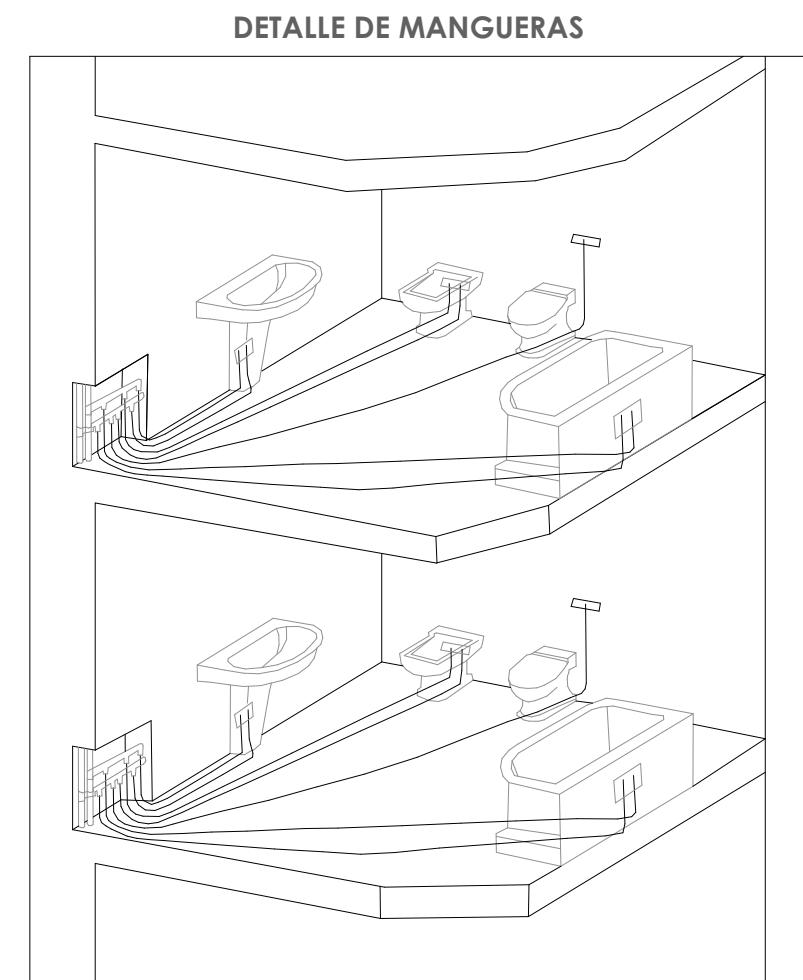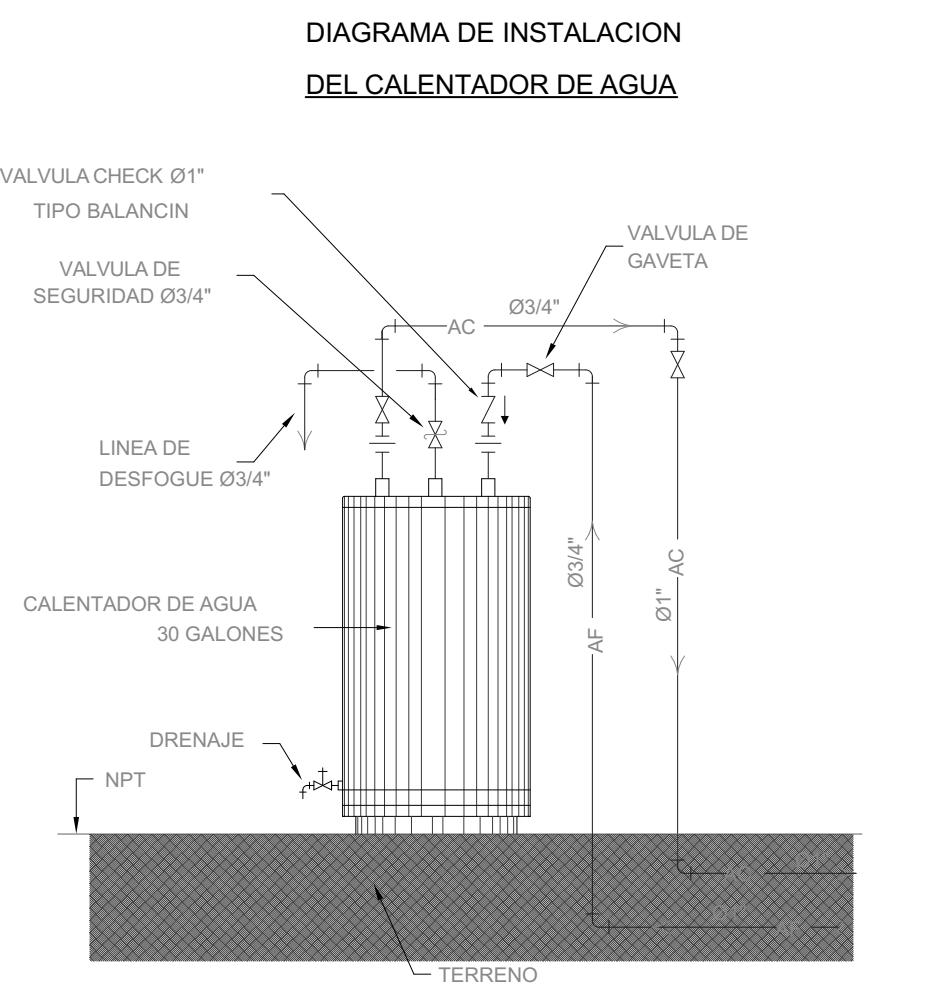